


# STADTKRONE DORSTEN

OBSERVATORIUM
JUNI 2018

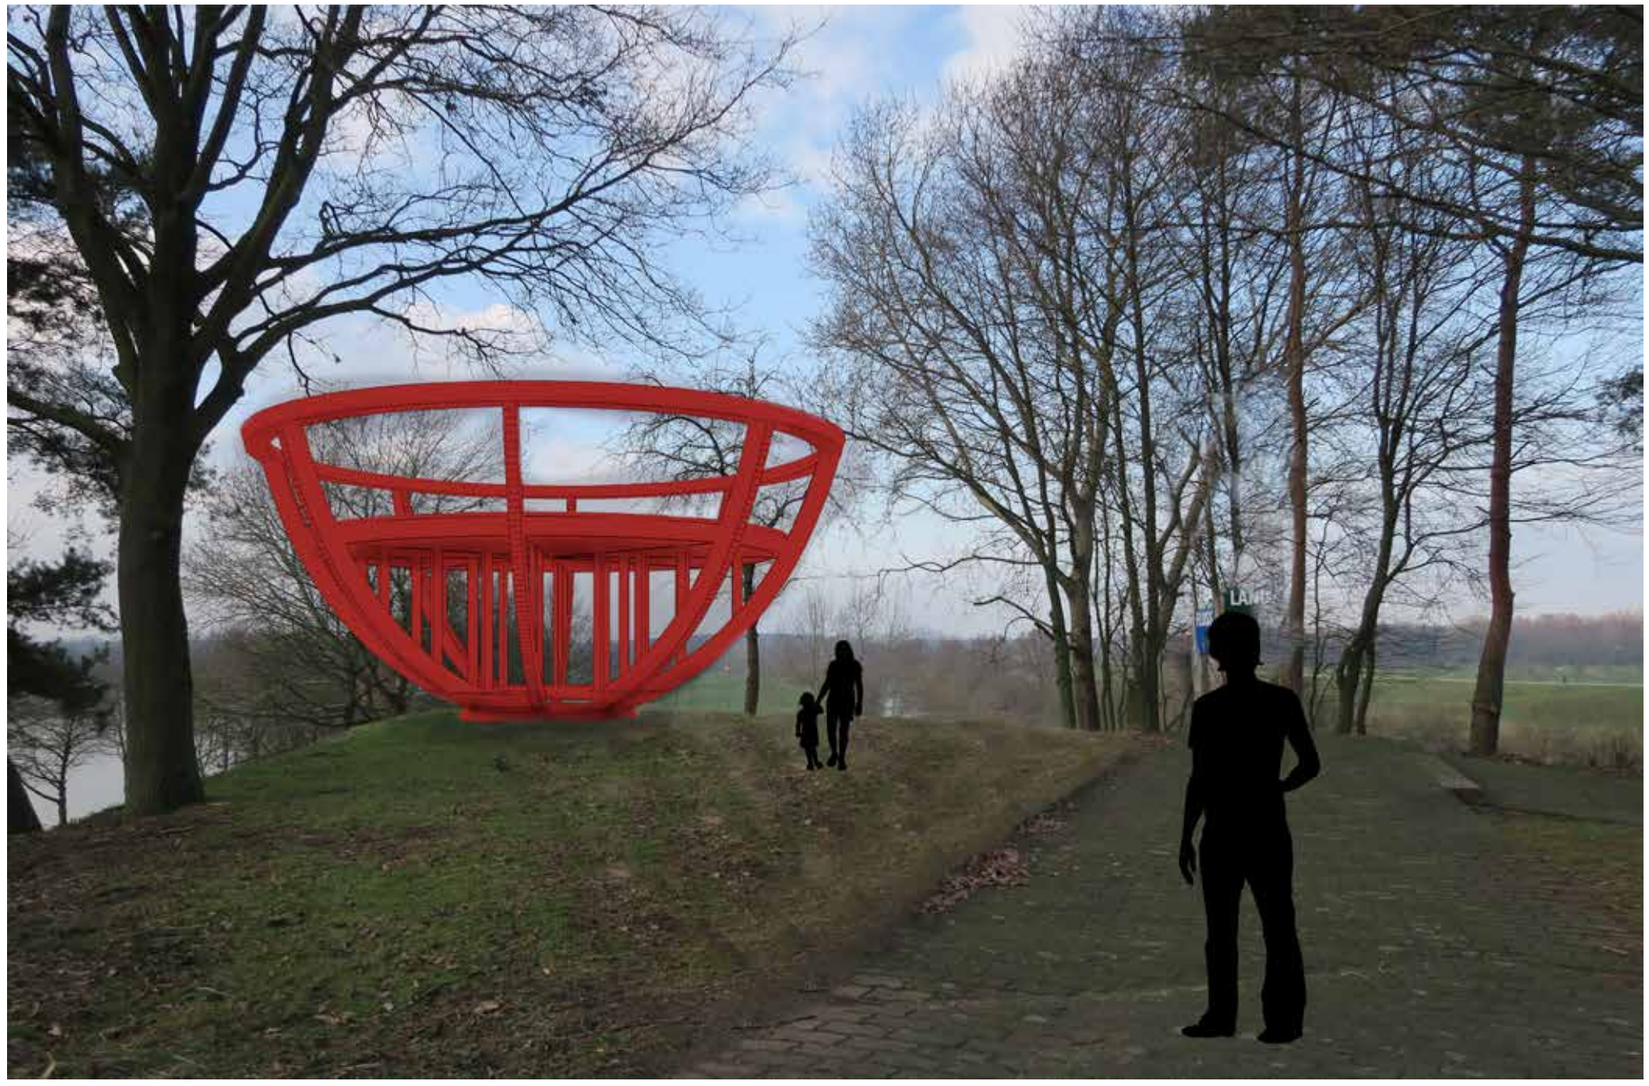

# STADTKRONE

Die Stadtkrone Dorsten ist eine zwischen den Bäumen hochragende Schale, die von weitem sichtbar ist. Die Schale öffnet sich zum Himmel hin und fängt das Regenwasser auf. Eine überdachte Rundbank bietet einen Blick auf die Umgebung und auf die Wassersäule, die bei Starkregen unter der Dachöffnung entsteht. Auf dem Plateau versickert das Regenwasser über zwei Wasserrinnen die den Wesel-Datteln-Kanal




# ANALYSE

IMPLUVIUM
SCHAAL







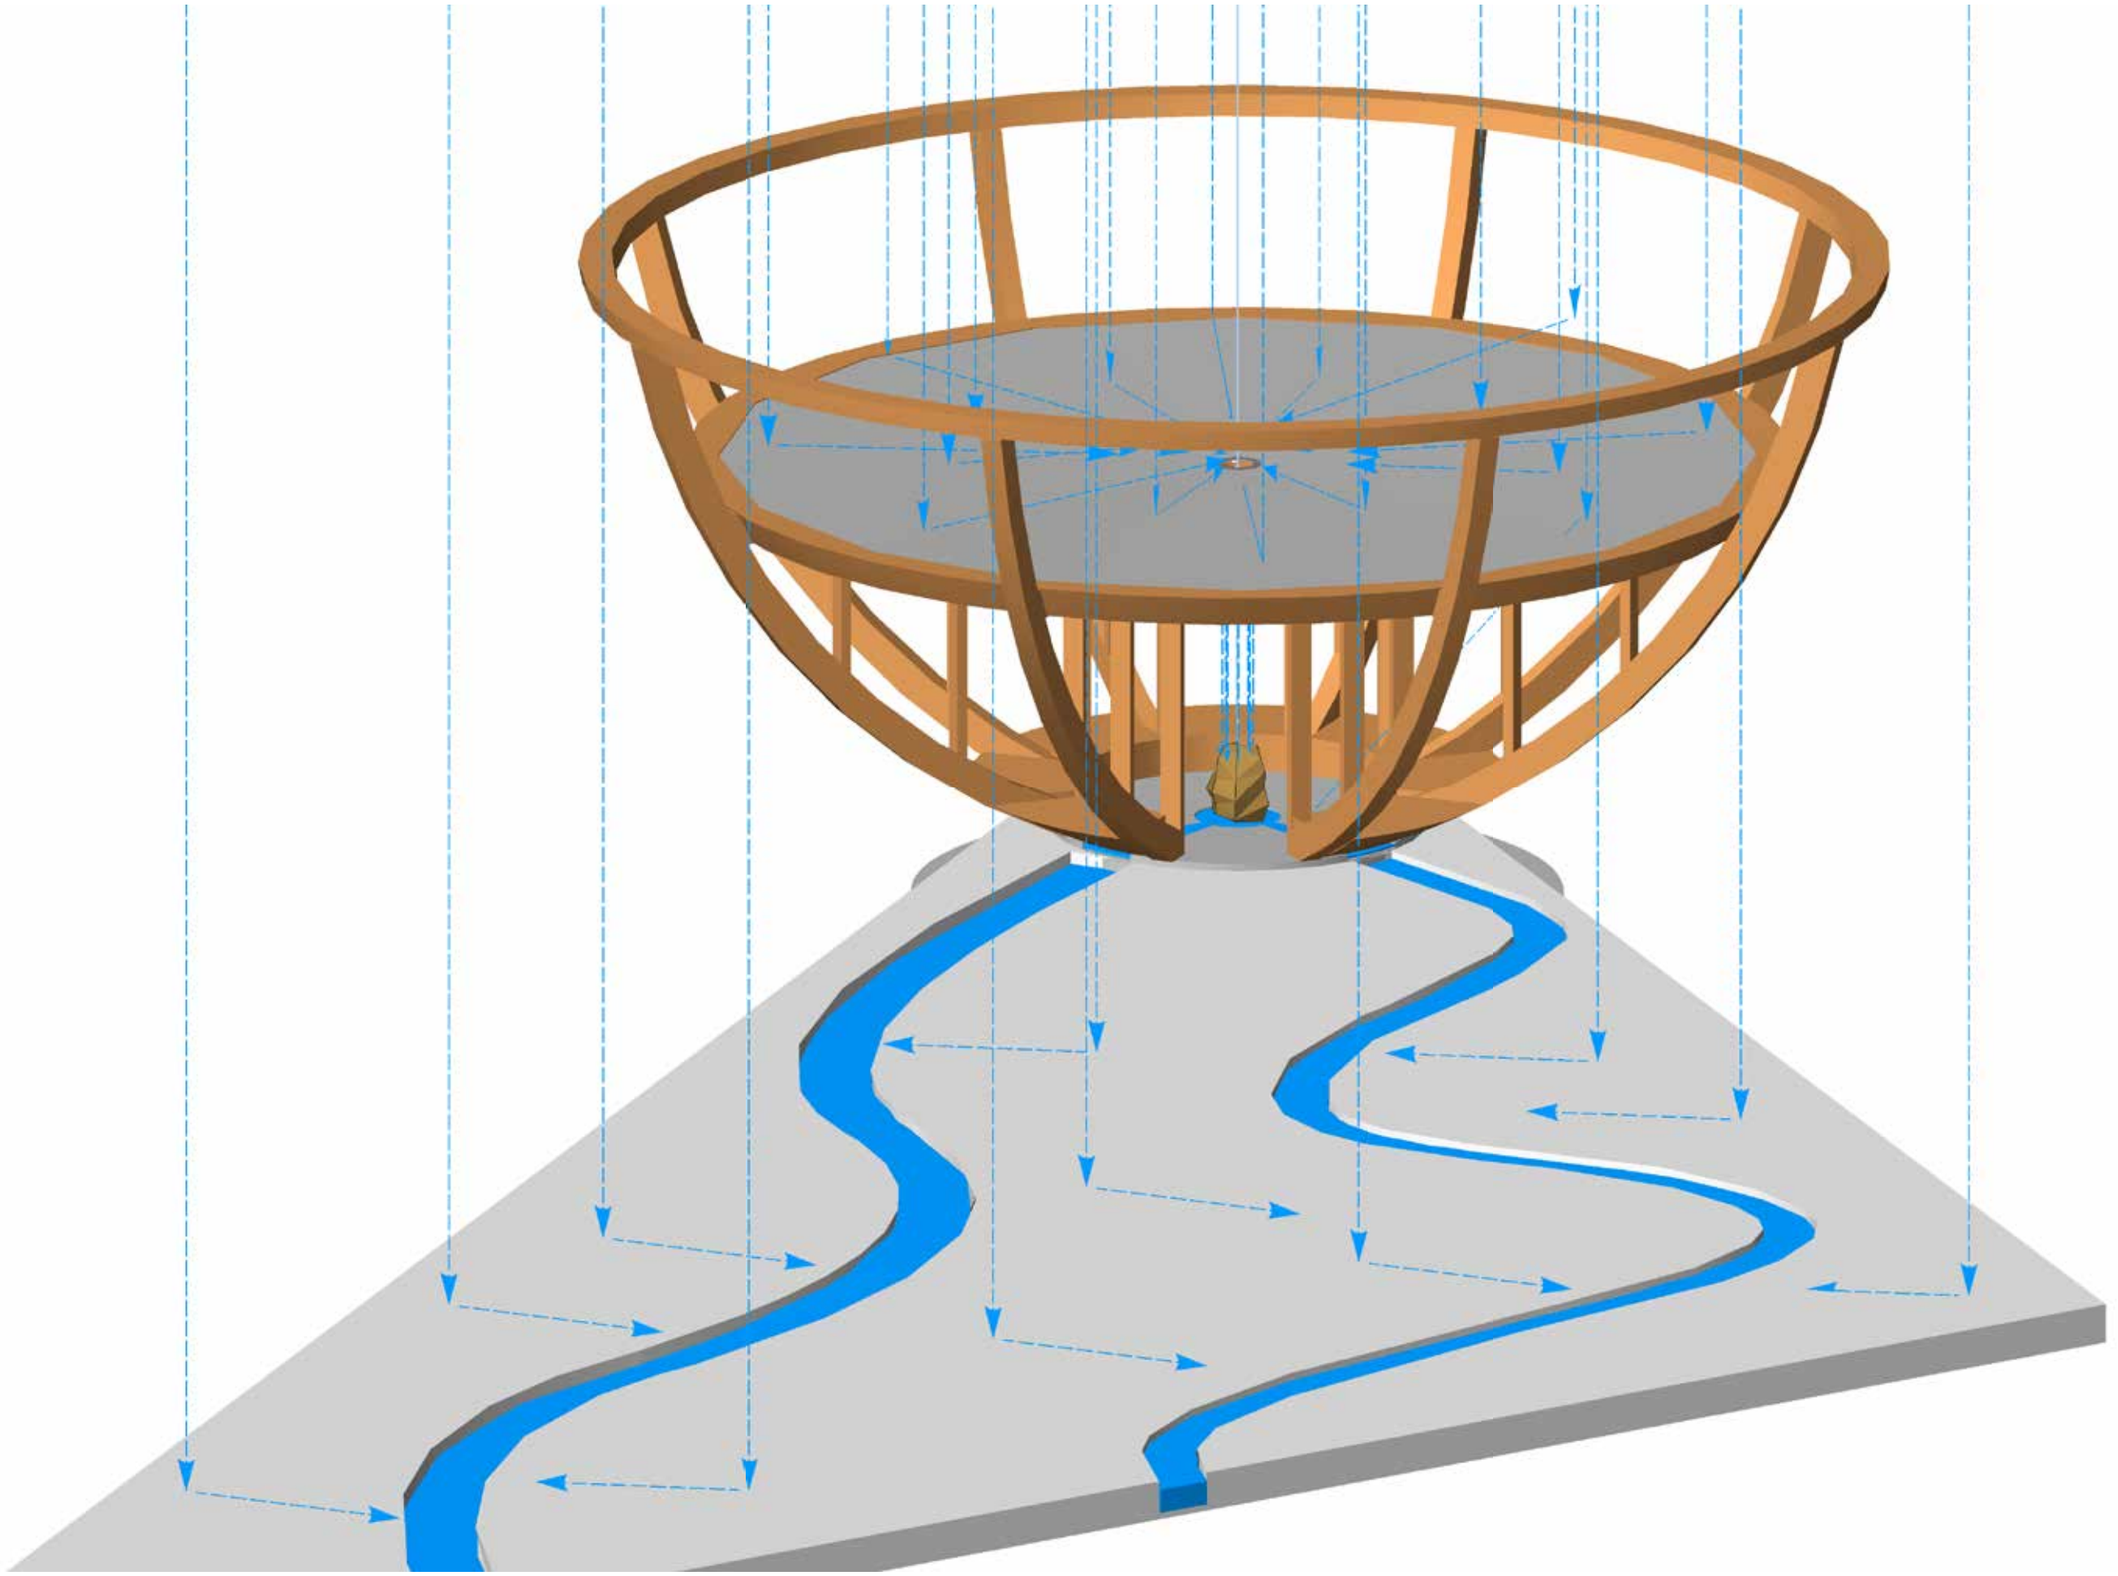

DACH


FRAME


BANK

STEIN


FUNDAMENT

PLATEAU

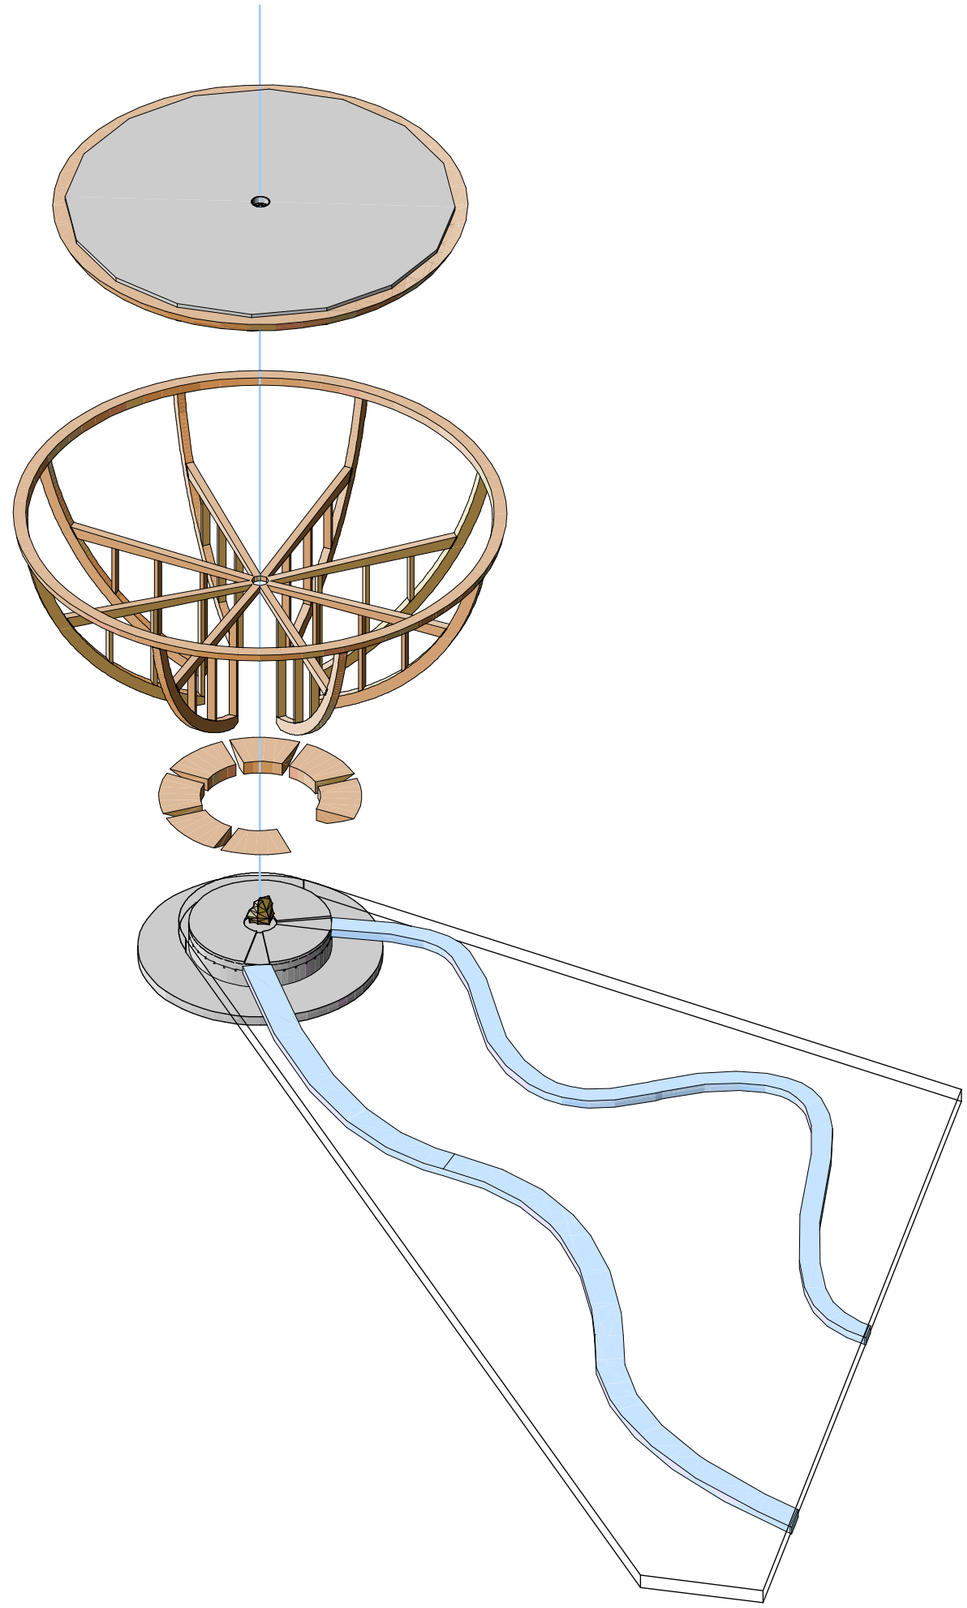


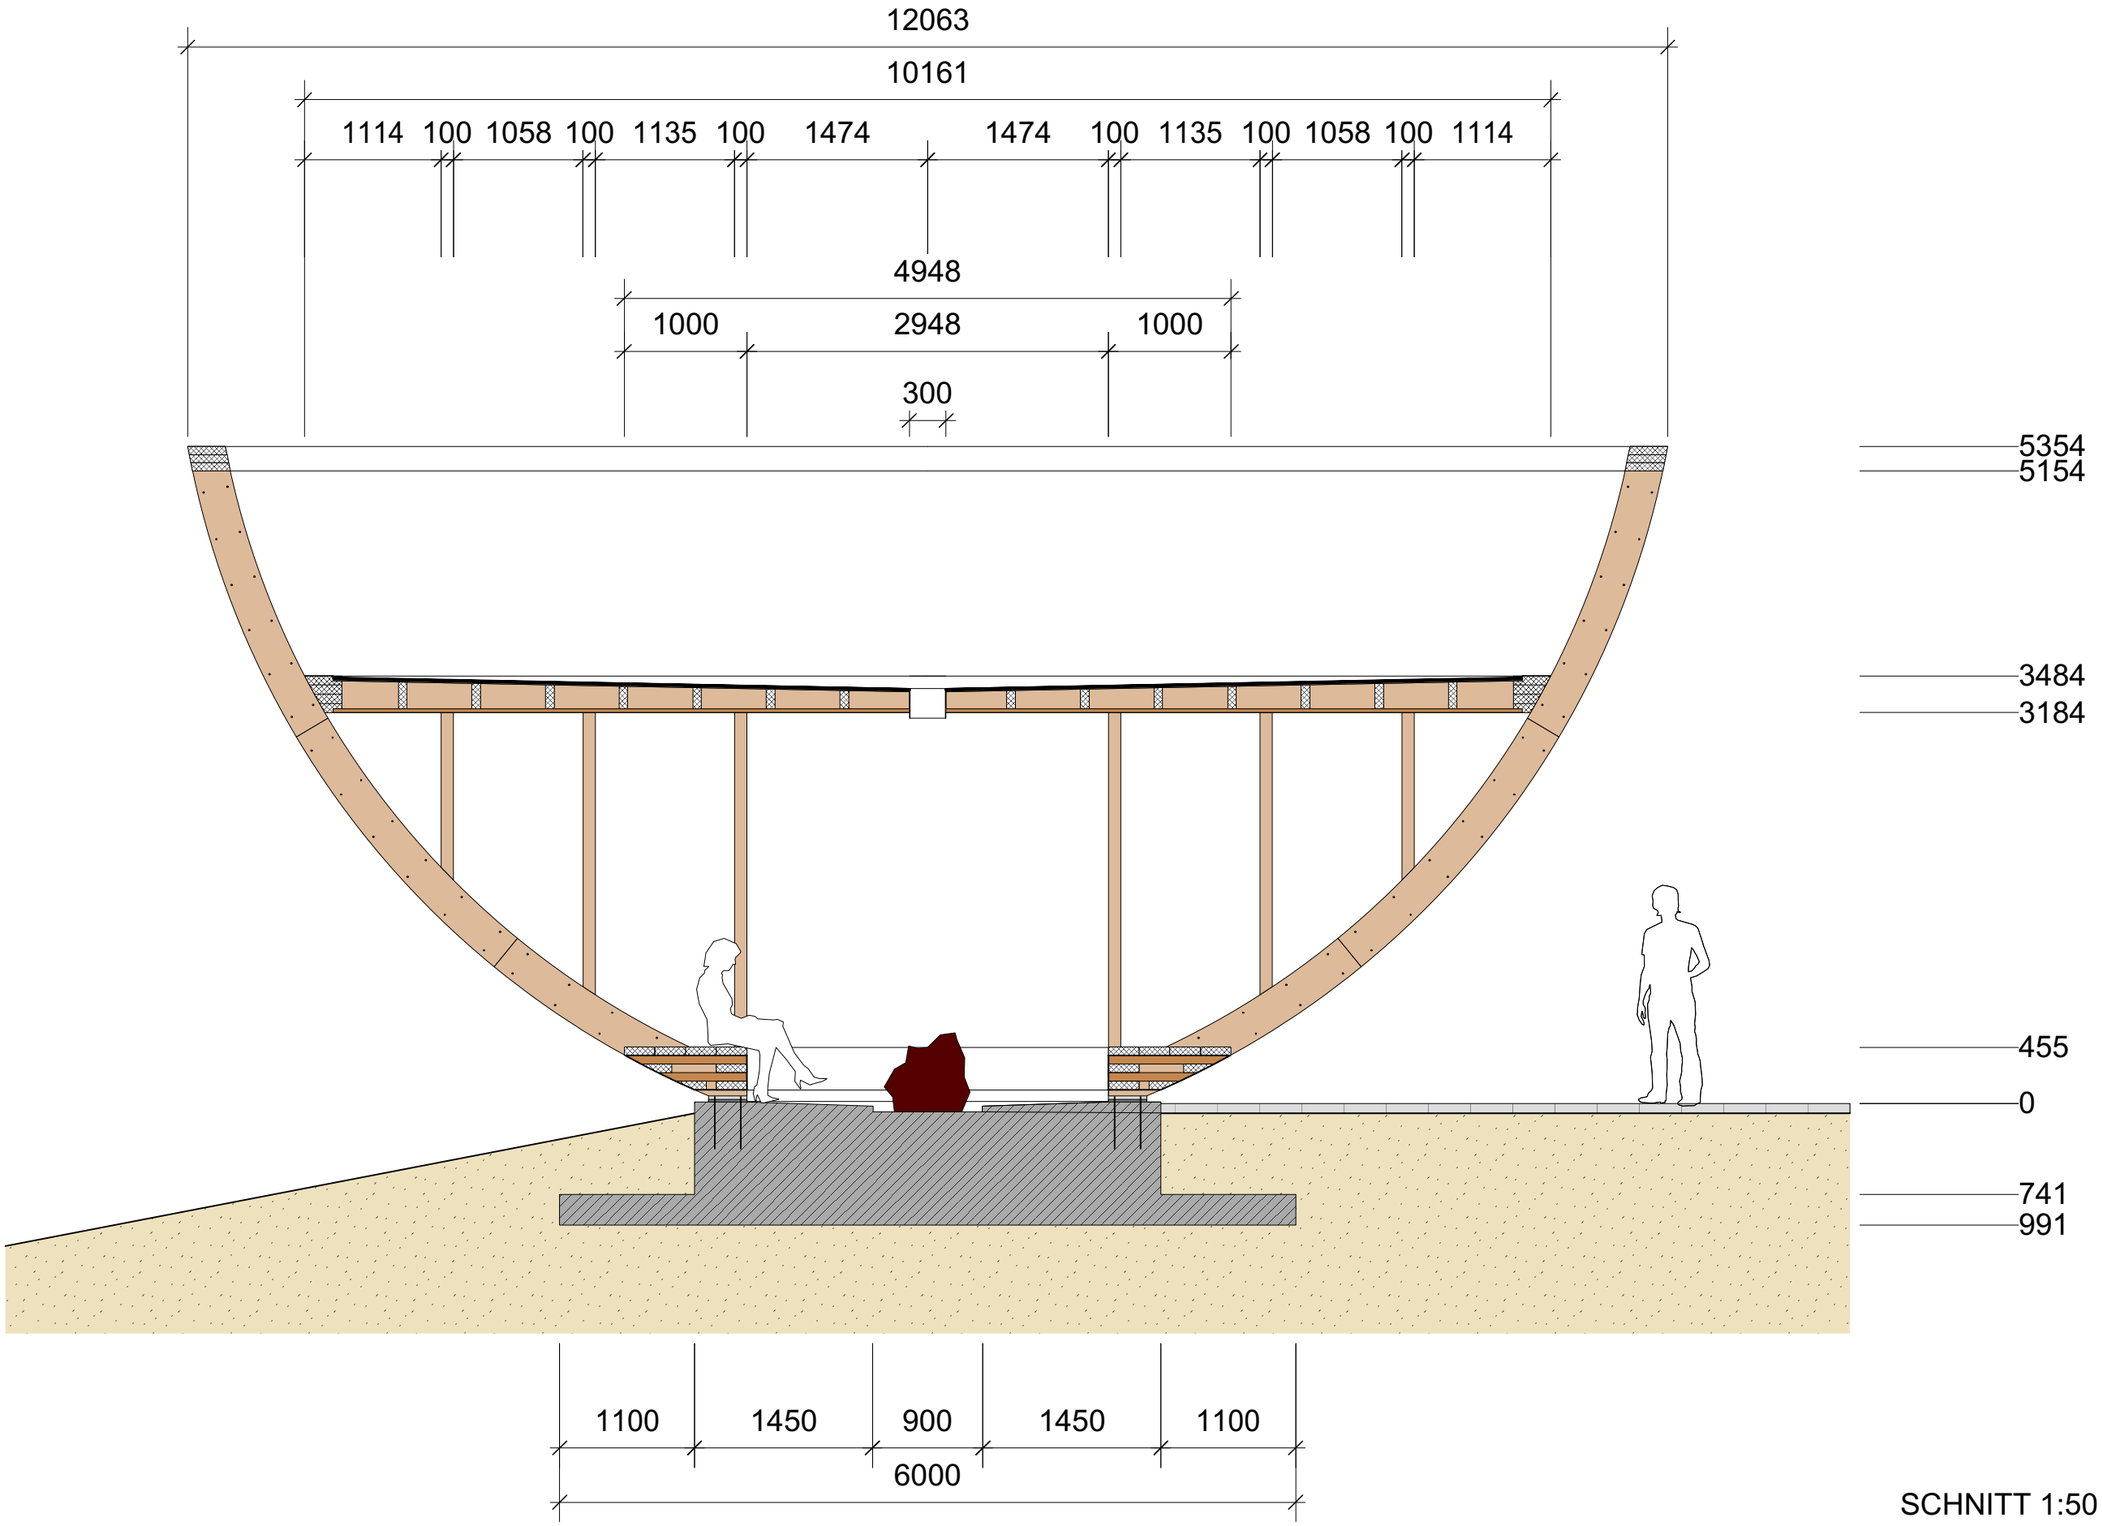
12063
10161
1114 100 1058 100 1135 100 1474 1474 100 1135 100 1058 100 1114
4948
1000 2948 1000
300
5354
5154
3484
3184
455
0
741
991
1100 1450 900 1450 1100
6000


SCHNITT 1:50

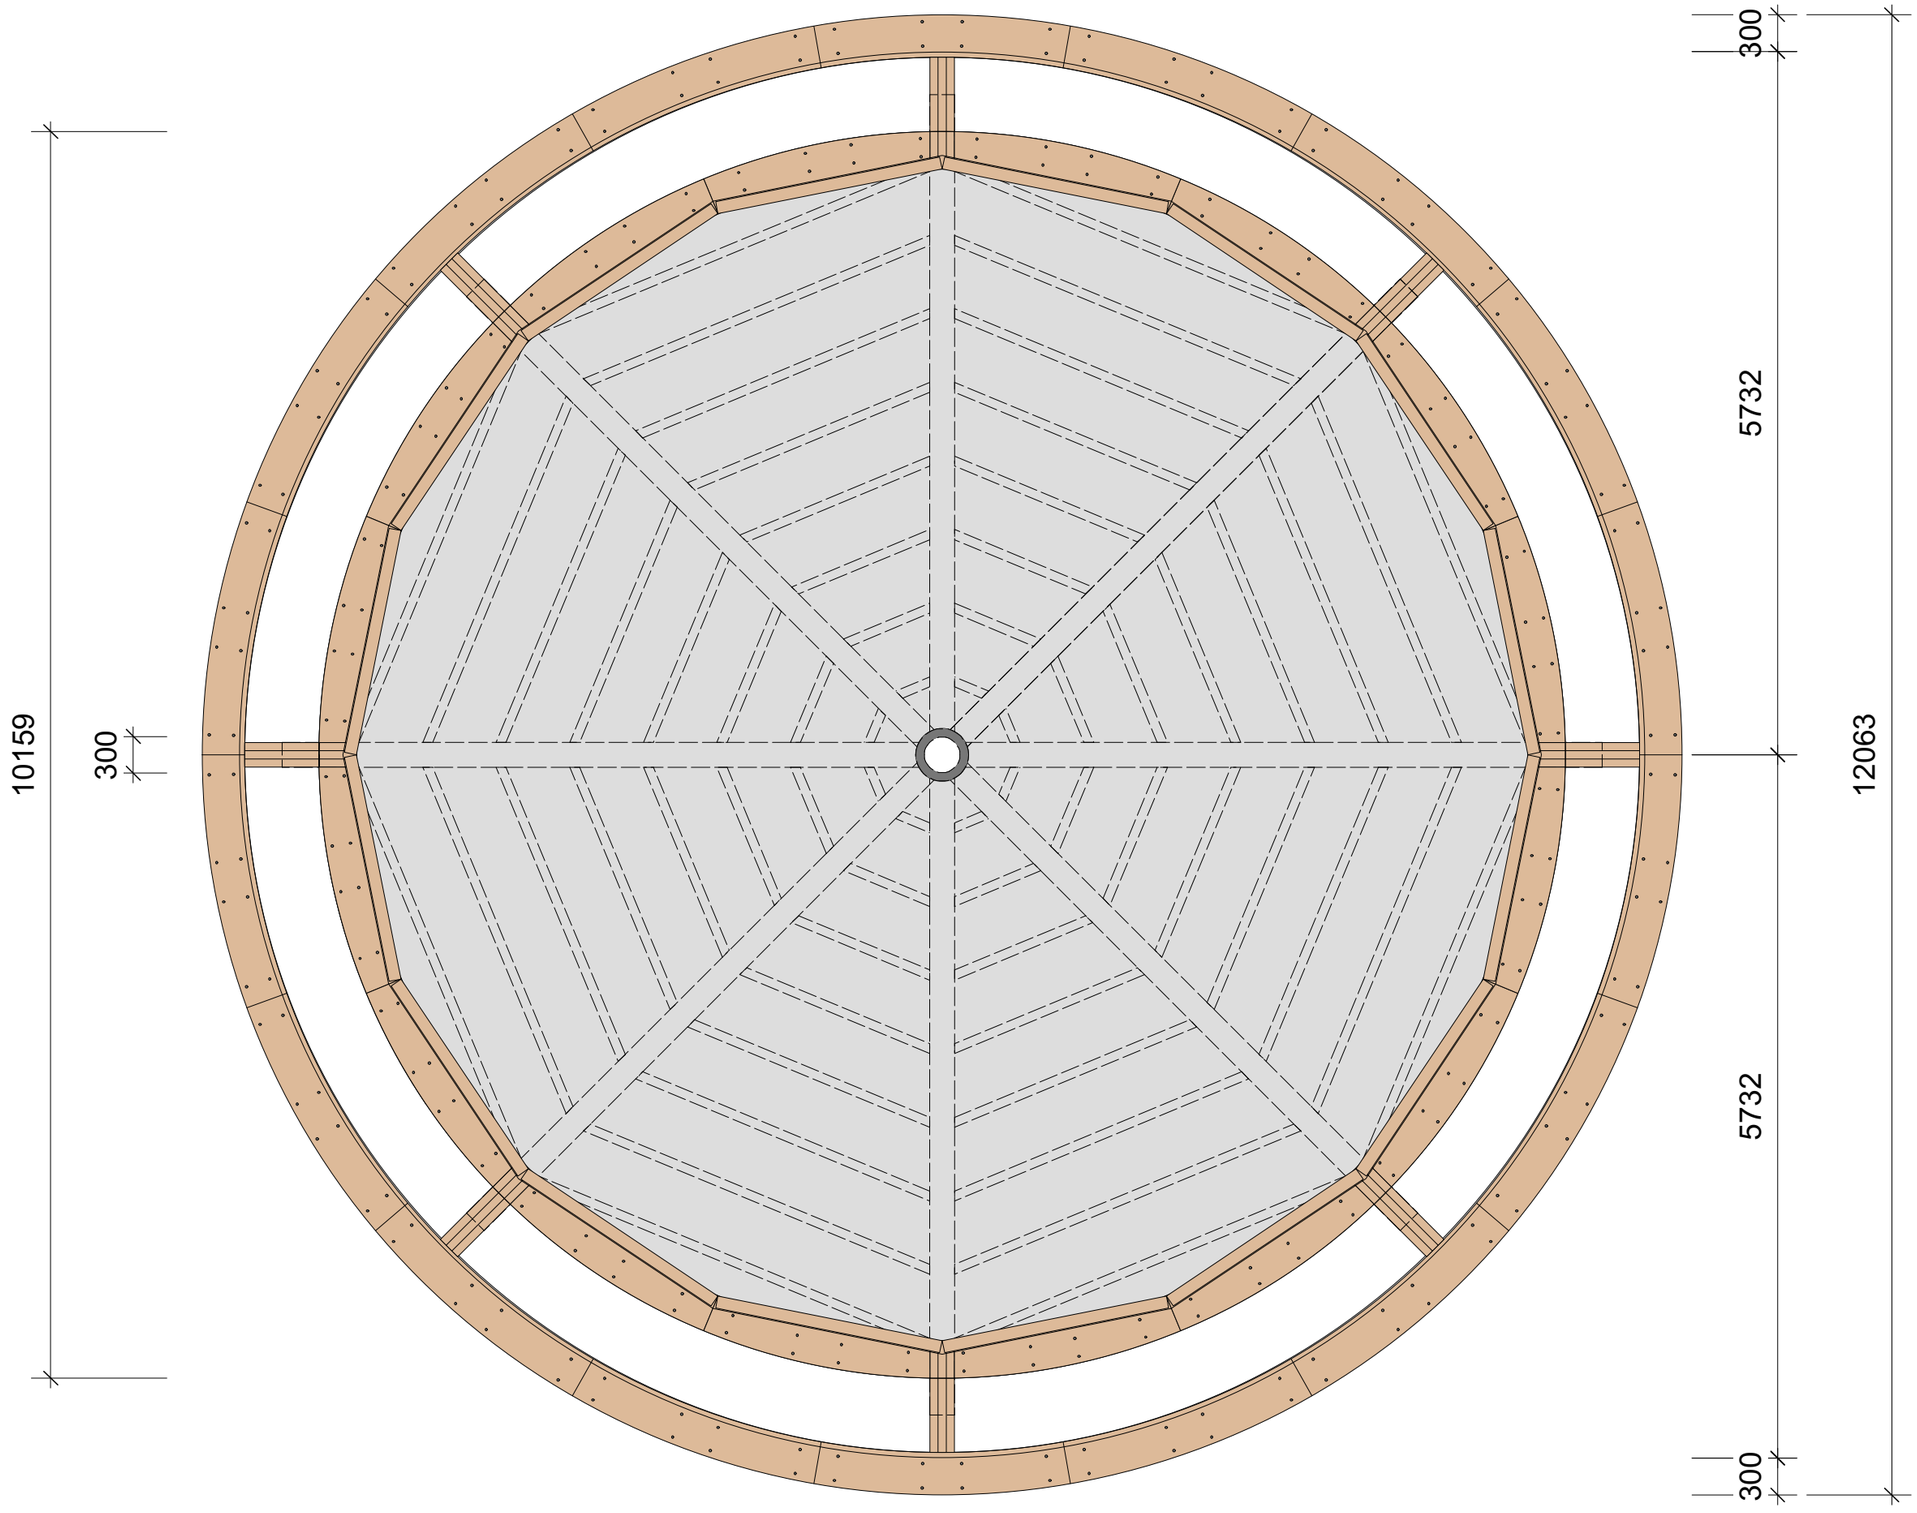



GRUNDRISS IM DACHBEREICH 1:50

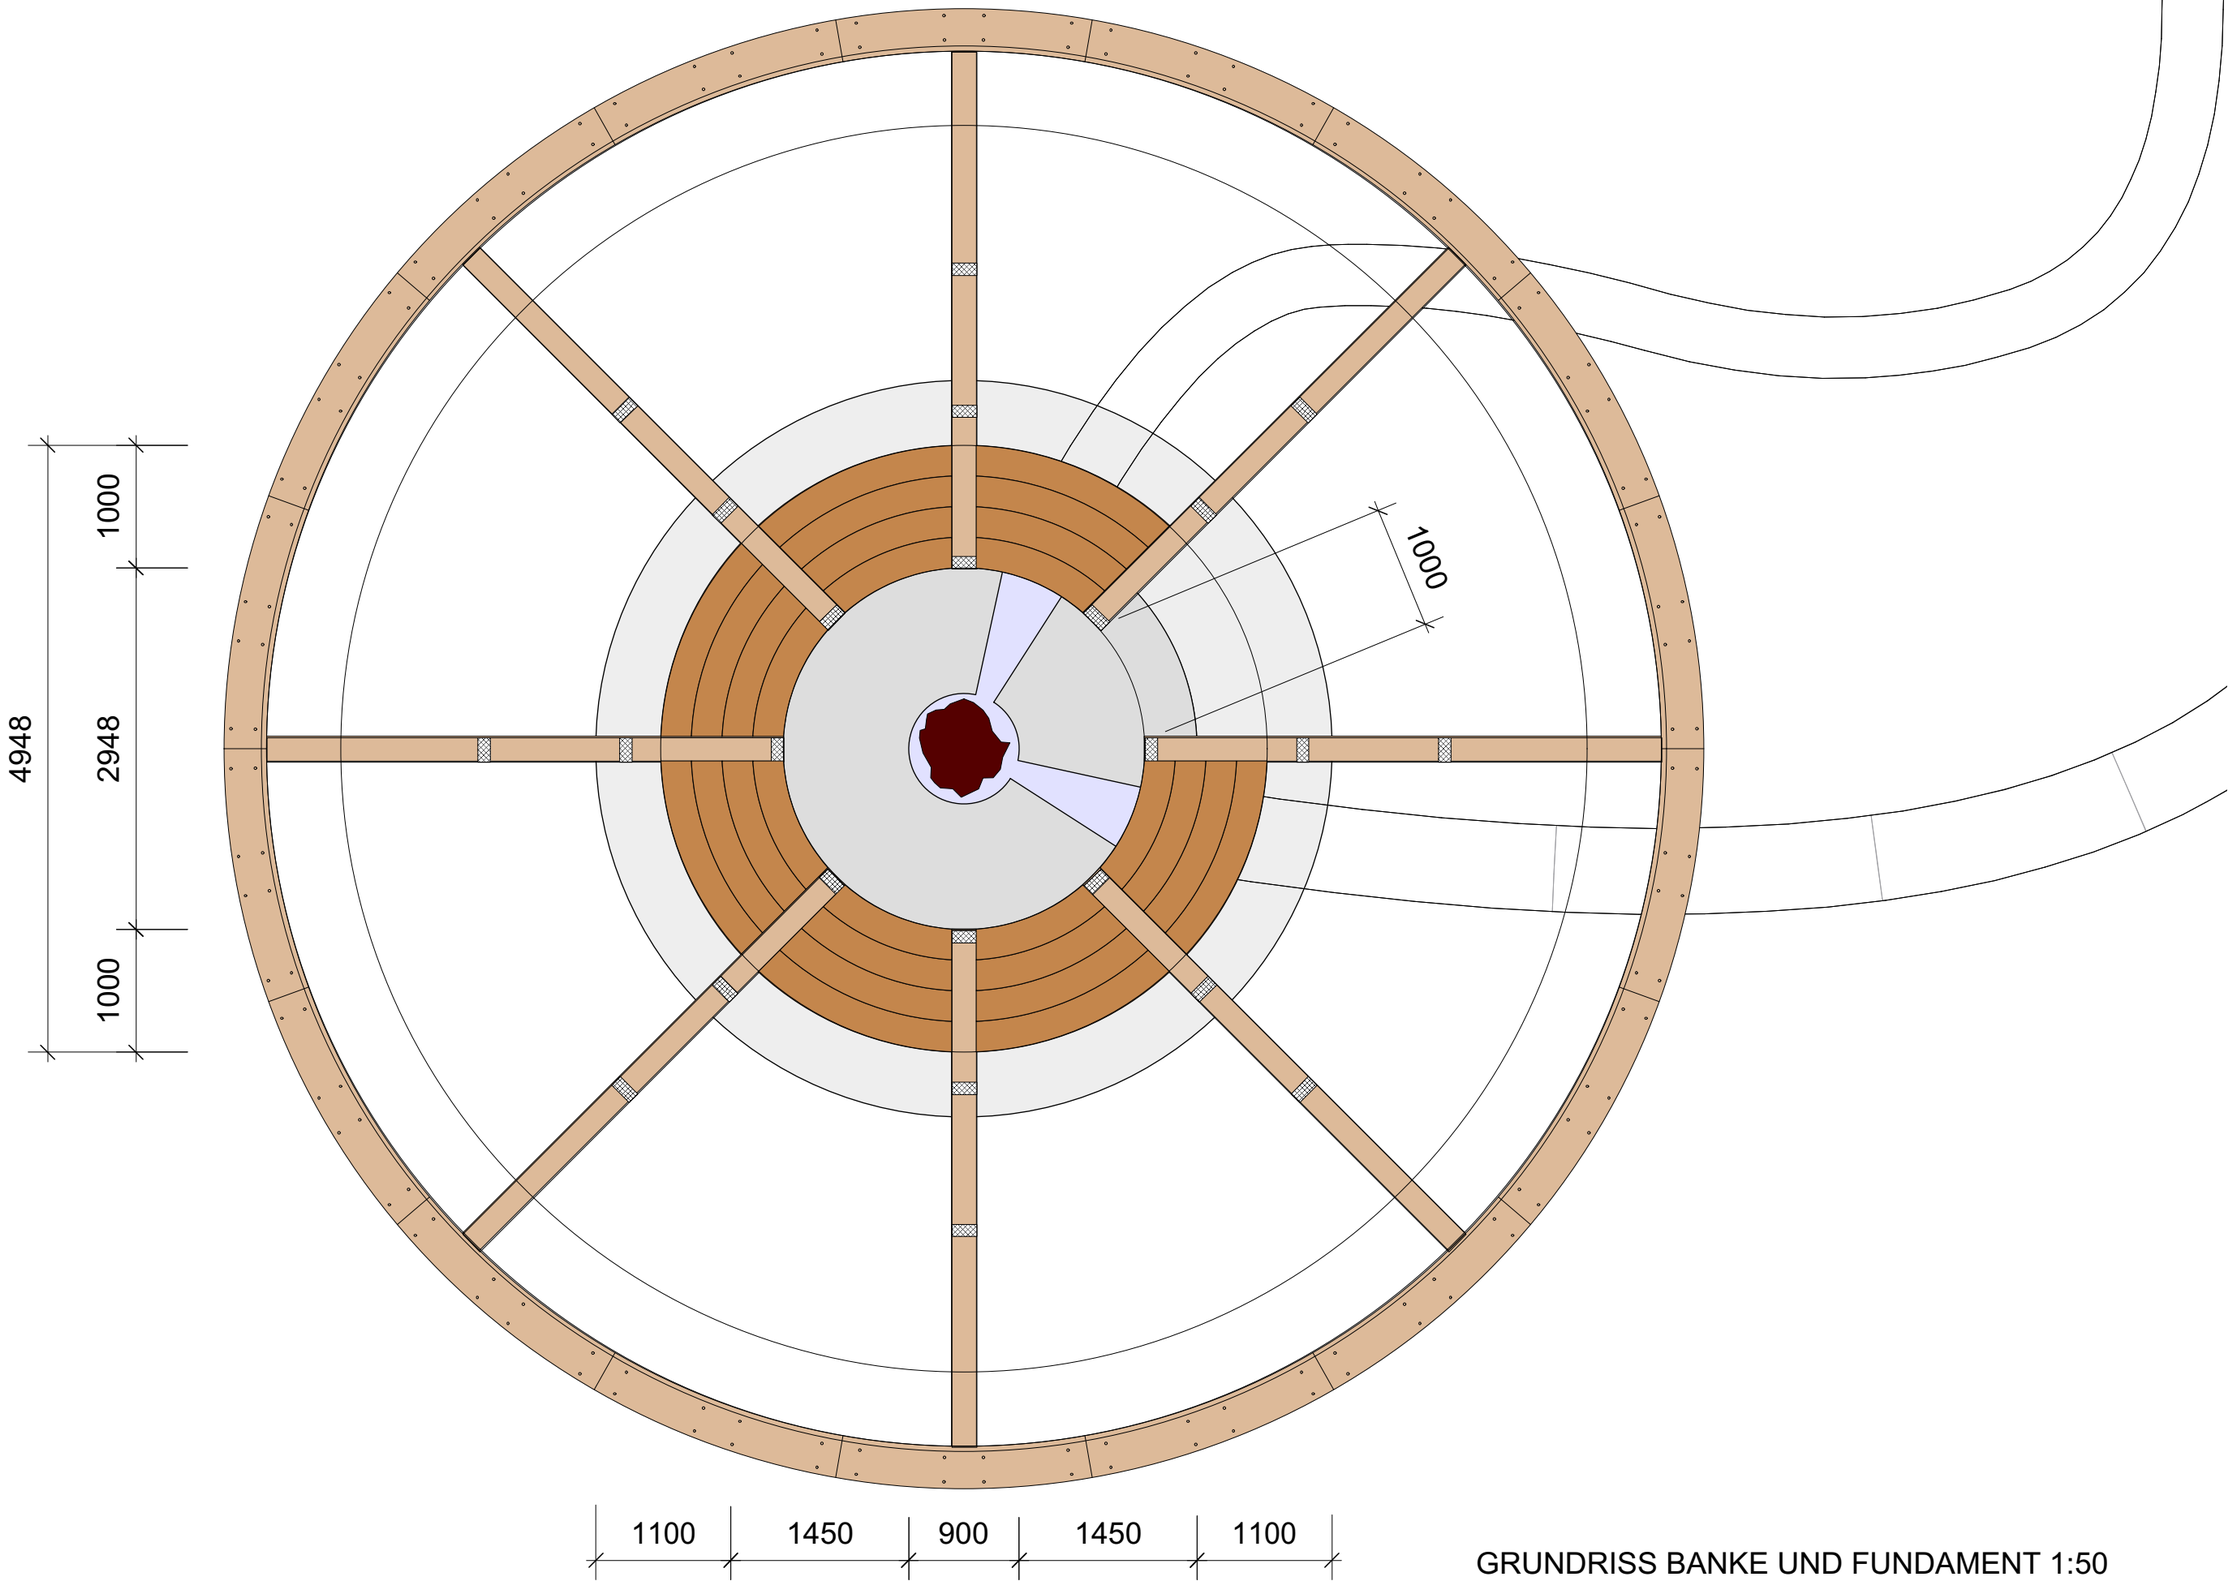




GRUNDRISS BANKE UND FUNDAMENT 1:50

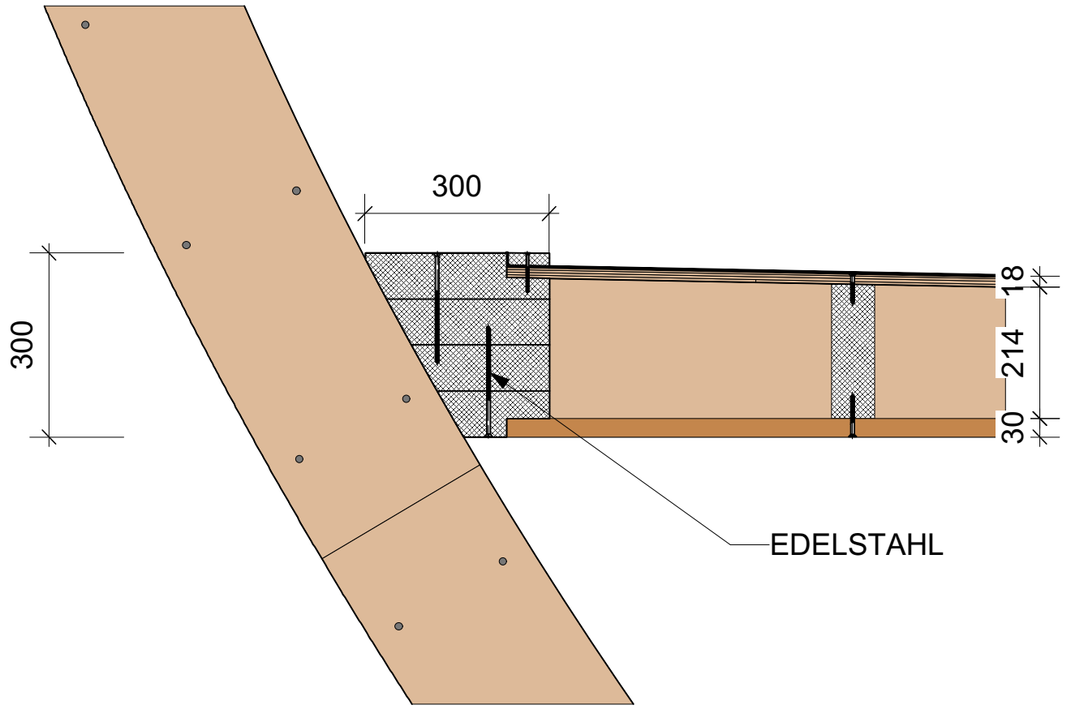
300
300
18
214
30
EDELSTAHL

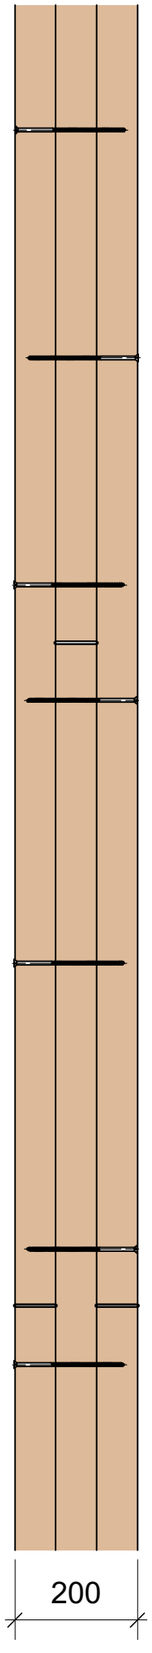


EDELSTAHL
180
50
200
50
50
200
300
50
67
67
67
200

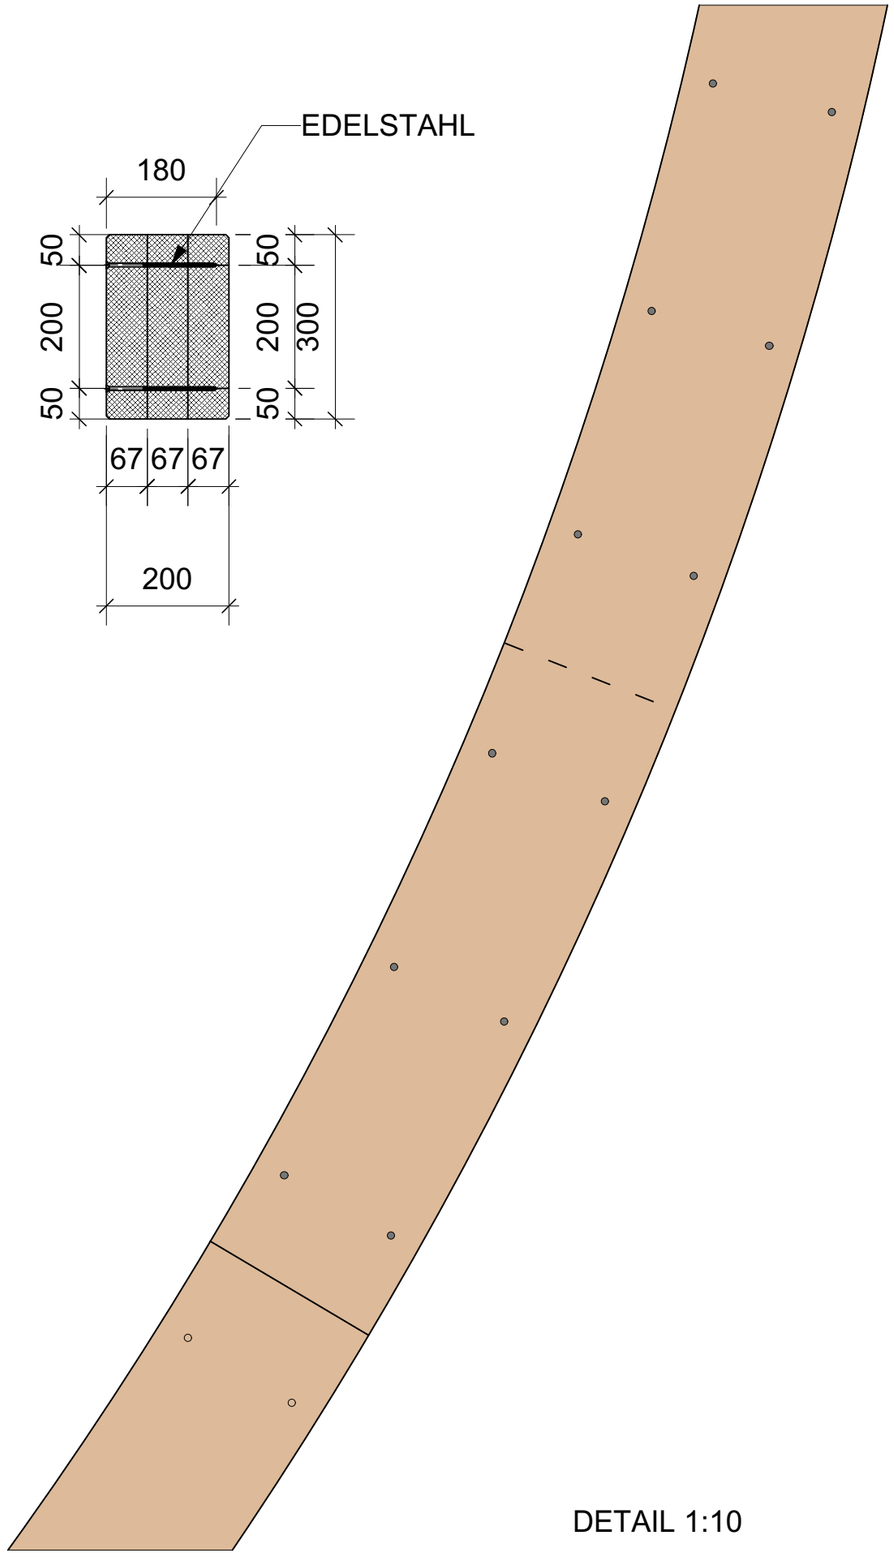

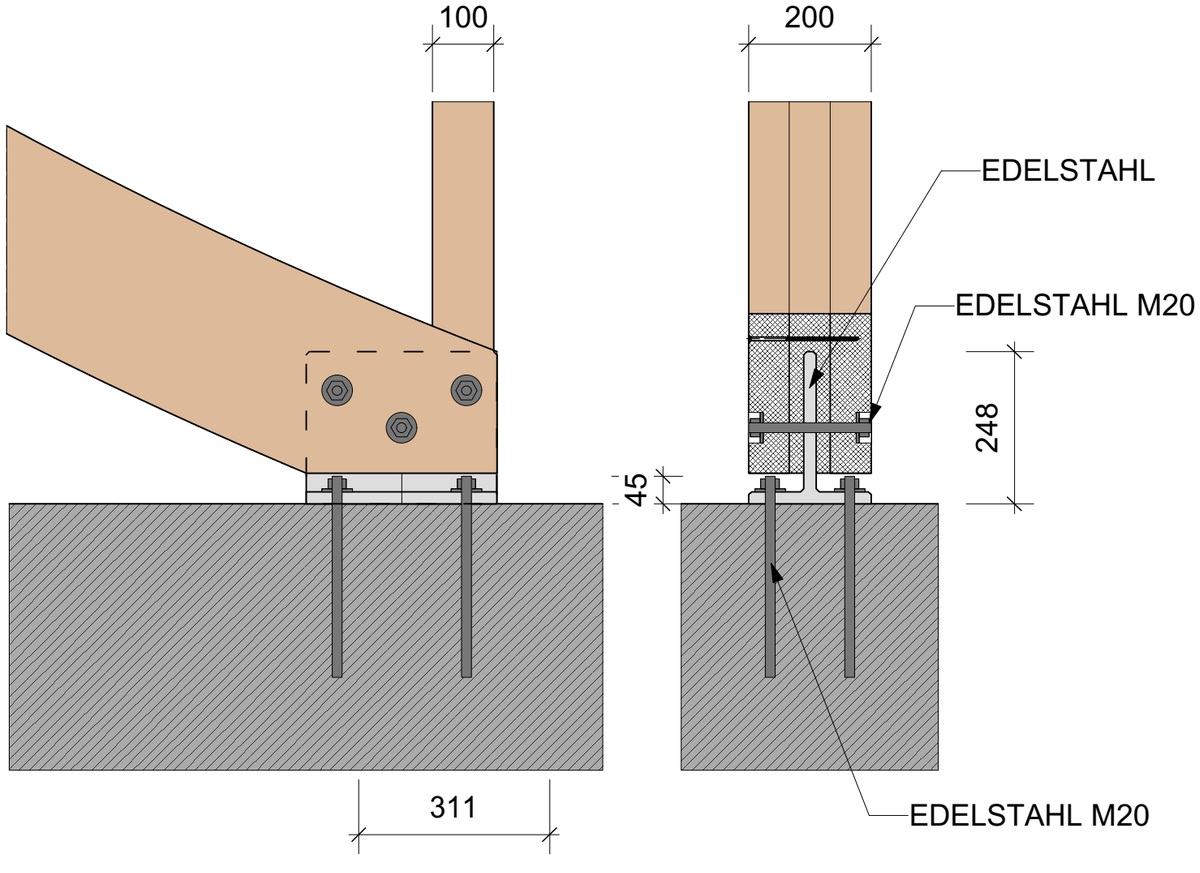
100
200
EDELSTAHL
EDELSTAHL M20
248
45
311
EDELSTAHL M20
200

DETAIL 1:10

