


ZANDPOORT

Definitief Ontwerp

OBSERVATORIUM
JANUARI 2018

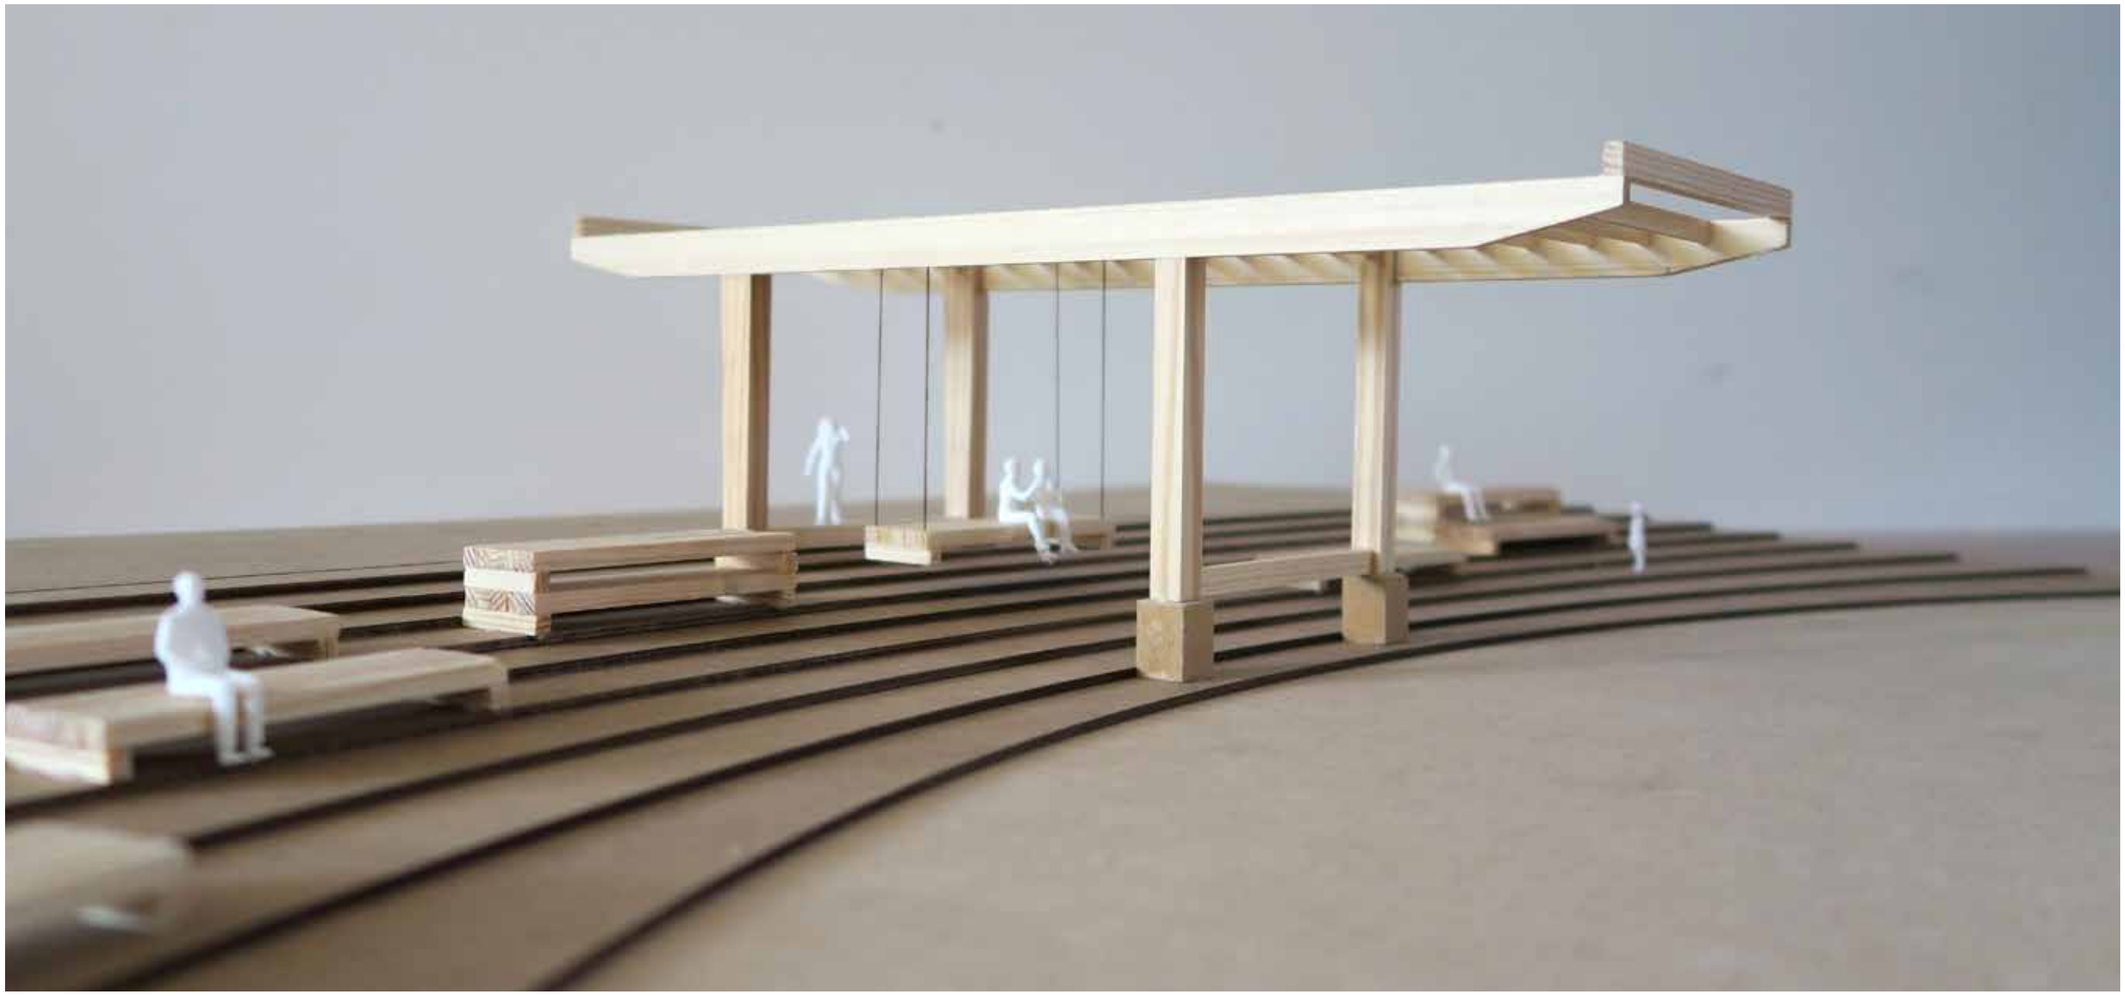


Zandpoort

De kunstenaars van Observatorium stellen voor om van de natuurlijke oevers aan de zwaaikom een strandje met een grote schommelpergola en zitbanken te maken. De vormgeving ervan wordt ontleend aan de rode majestueuze kranen en de stapels containers van de Barge Terminal Tilburg aan de overzijde van het Wilheminakanaal.

Kraan

De schommelpergola, in de vorm van een containerkraan, is gemaakt van rood geverfd hout en meet ongeveer 15 meter lang en 5 meter hoog en breed. Door een derde identieke kraan zonder industriële functie aan de recreatieve kant van het kanaal te plaatsen ontstaat een omarming van het kanaal. De anonieme overslag aan de overkant wordt deel van een theatrale opstelling waarbinnen het schouwspel van het laden en lossen en het komen en gaan van de schepen plaatsvindt.

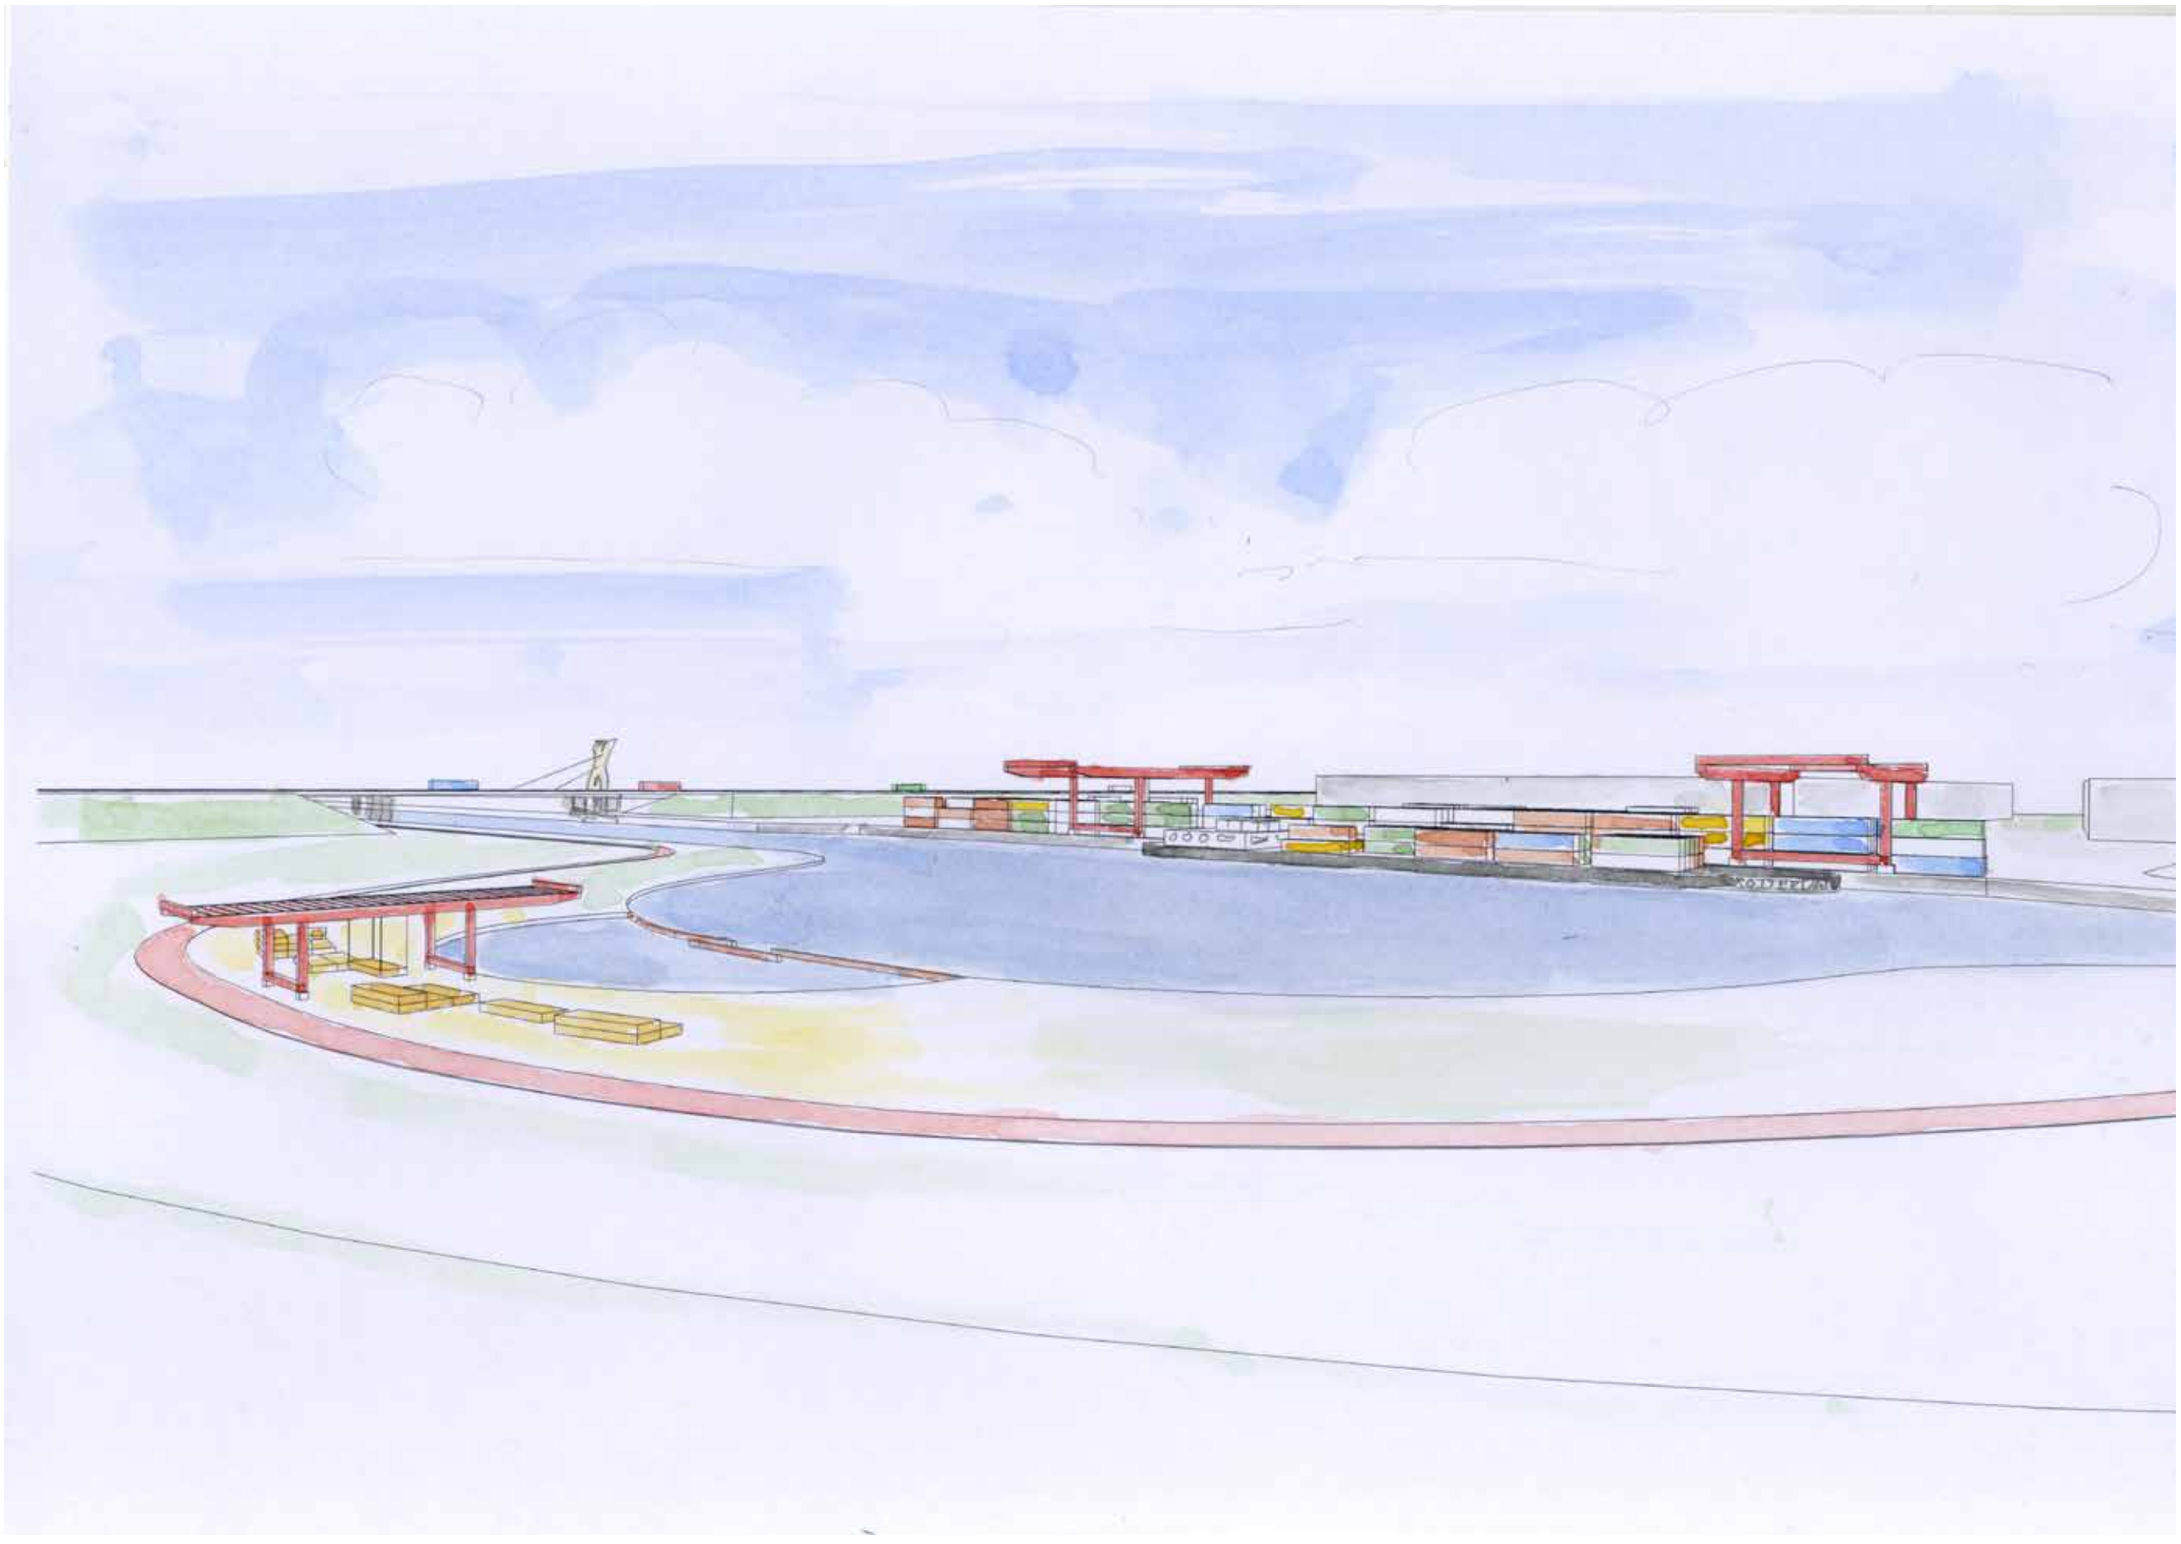



Schommel

In plaats van een container hangt er een rustbed aan de kabels van de kraanpergola. Deze hangplek haakt aan op de lange traditie van parkaanleg om schommels te maken voor een lichamelijke ontspanning. De passant luiert en schommelt in een sculpturale, klassieke en ambachtelijk gemaakte houtconstructie, met een fantastisch uitzicht op de Rotterdamse haven van Tilburg. De gebruiker bekruipt het gevoel zélf lading in een kraan te zijn en en het spiegelbeeld van de Barge Terminal te vormen. Het roept een verwondering op die uitstijgt boven de waardering voor de omgeving en het vakwerk van het kunstwerk.




Zwemplek

Rondom Tilburg zijn vele zwemplekken in vennen en plassen. Het zou prachtig zijn als deze zomerse ontspanning ook aan het zwaaikomstrand kan plaatsvinden. De in het zand verzonken zitbanken, met het uiterlijk van containers bieden tevens beschutting en nodigen kinderen uit tot spel. Over enkele jaren is de bomenrij langs Kanaaldijk Zuid volgroeid en ontstaat er een evenwicht tussen de grote groene bomen en de rode houtconstructie. Vanaf de groene dijk heb je een fantastisch uitzicht op de drie rode kranen en de witte brug, symbolen van onze welvaart en zorg voor de omgeving.





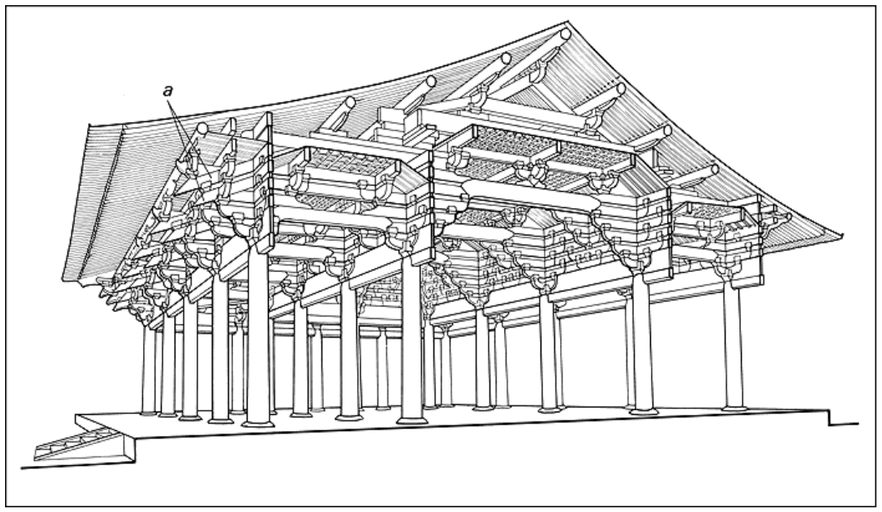

Park


De containerkranen lijken sterk op de Japanse en Chinese poorten die ingangen van parken markeren. De Zandpoort verleent het gevoel dat de langgerekte ruimte langs het kanaal onderbroken wordt door een park dat in het zuiden begrensd wordt door de monding van de Donge en in het noorden door de tuibrug over het Wilhelminakanaal. In het westen wordt het Zandpoortpark afgesloten door een dijklichaam en in het oosten door een wand van containers. Met één eenvoudig gebaar van een kraan als parkpaviljoen wordt de omgeving anders gelezen en ervaren.




Kanaal

Op het kanaal is het een drukte van belang met de barges, die zes maal per dag de terminal aandoen. Door als passant en recreant onder je eigen kraan te zitten ontstaat er een verbondenheid met de schippers en de goederenoverslag, die verbonden is met het wereldwijde transportnetwerk. Het kanaal is op te vatten als de grens van een ontoegankelijke wereld, de Zandpoort maakt er een schouwtoneel van. En wat voorheen uitsluitend als industrie herkend werd, maakt nu deel uit van de monumentale stadsentree van Tilburg en de Reeshof.



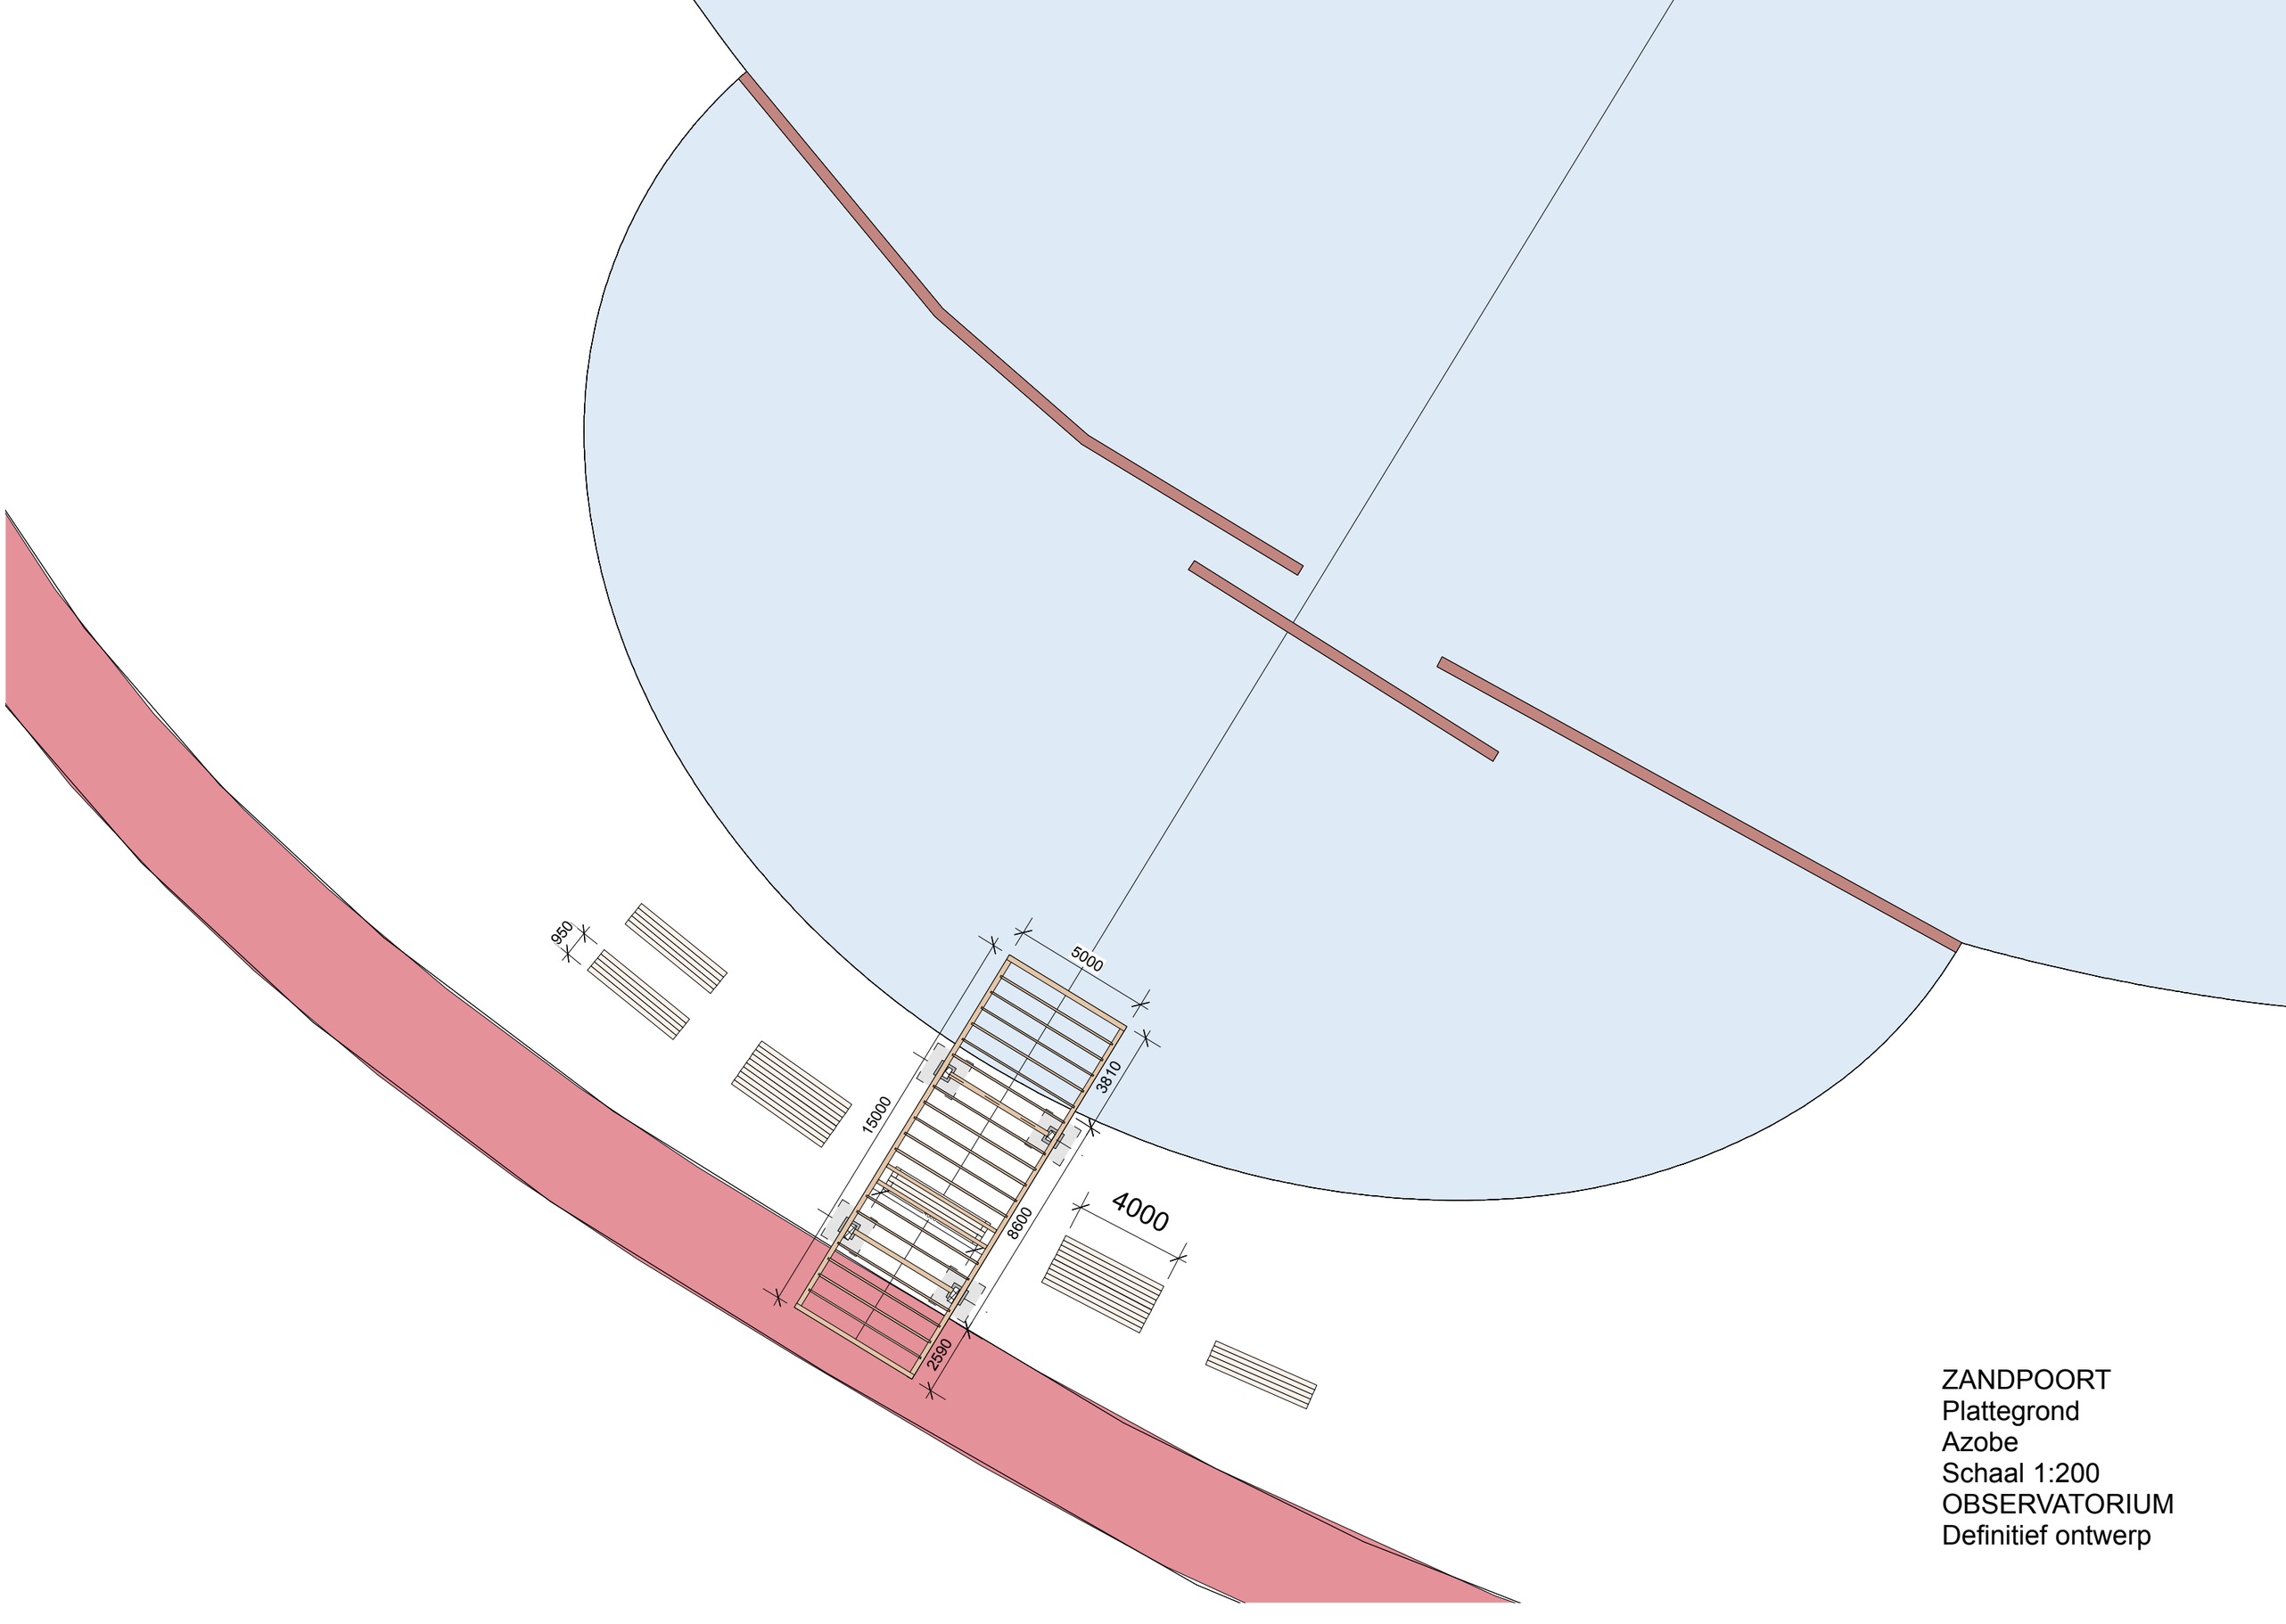

ZANDPOORT
Plattegrond
Azobe
Schaal 1:200
OBSERVATORIUM
Definitief ontwerp

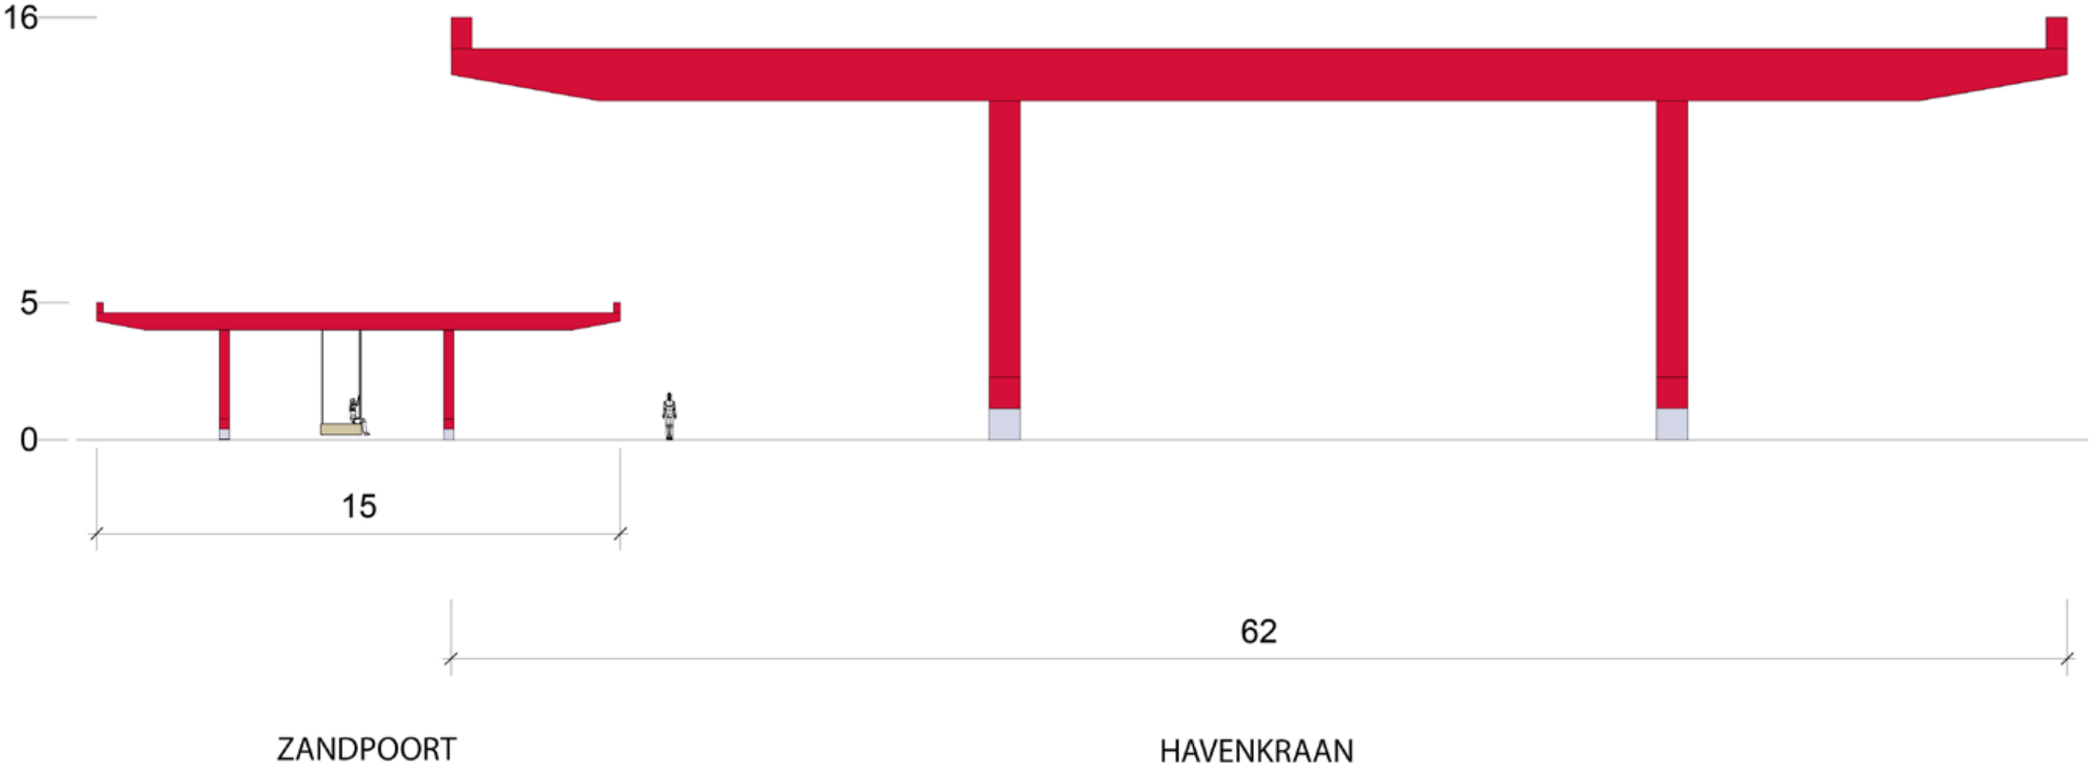
16
5
0
15
62
ZANDPOORT
HAVENKRAAN

Techniek en uitvoering

De Zandpoort wordt uitgevoerd in Azobe, een uiterst duurzame houtsoort, met FSC-keurmerk.

De grote balken en kolommen worden samengesteld uit balken die onderling verbonden worden d.m.v. thermisch verzinkte stalen stiften en draadeinden.

Het geheel wordt behandeld met een rode beits, die niet kan afbladderen.

De banken en schommel worden uitgevoerd in Douglas balken, onderling verbonden met thermisch verzinkte draadeinden, en blank geïmpregneerd.

Zowel de poort als de banken worden gefundeerd op betonnen prefab-elementen. De schommel wordt voorzien van een kabel zodat die niet al te ver heen en weer kan bewegen.

De onderdelen worden aangevoerd per vrachtwagen en geplaatst met een kraan


Levertijd: ca. 10 weken

Poort


Houtsoort	:	Azobé, kwaliteit volgens NEN 5493, vers gezaagd Geleverd met FSC 100% (SGSCH-COC-000790)
Totale lengte	:	15 m
Breedte	:	5,00 m
Hoogte	:	ca. 4,50 m
Afwerking	:	vierzijdig geschaafd
Verbindingsmiddelen	:	Fe 360, thermisch verzinkt
Schilderen	:	1x kleurconservering Induline GW310
Onderbouw	:	4 stuks betonpoeren

Zitbanken (10 stuks incl. schommel)


Houtsoort	:	Douglas Geleverd met FSC 100% (SGSCH-COC-000790)
Totale lengte	:	4,00 m
Breedte	:	0,95 m
Hoogte	:	0,4 m
Afwerking	:	vierzijdig geschaafd
Verbindingsmiddelen	:	Fe 360, thermisch verzinkt
Schilderen	:	1x blanke conservering Induline GW310
Onderbouw	:	2 stuks betonpoeren

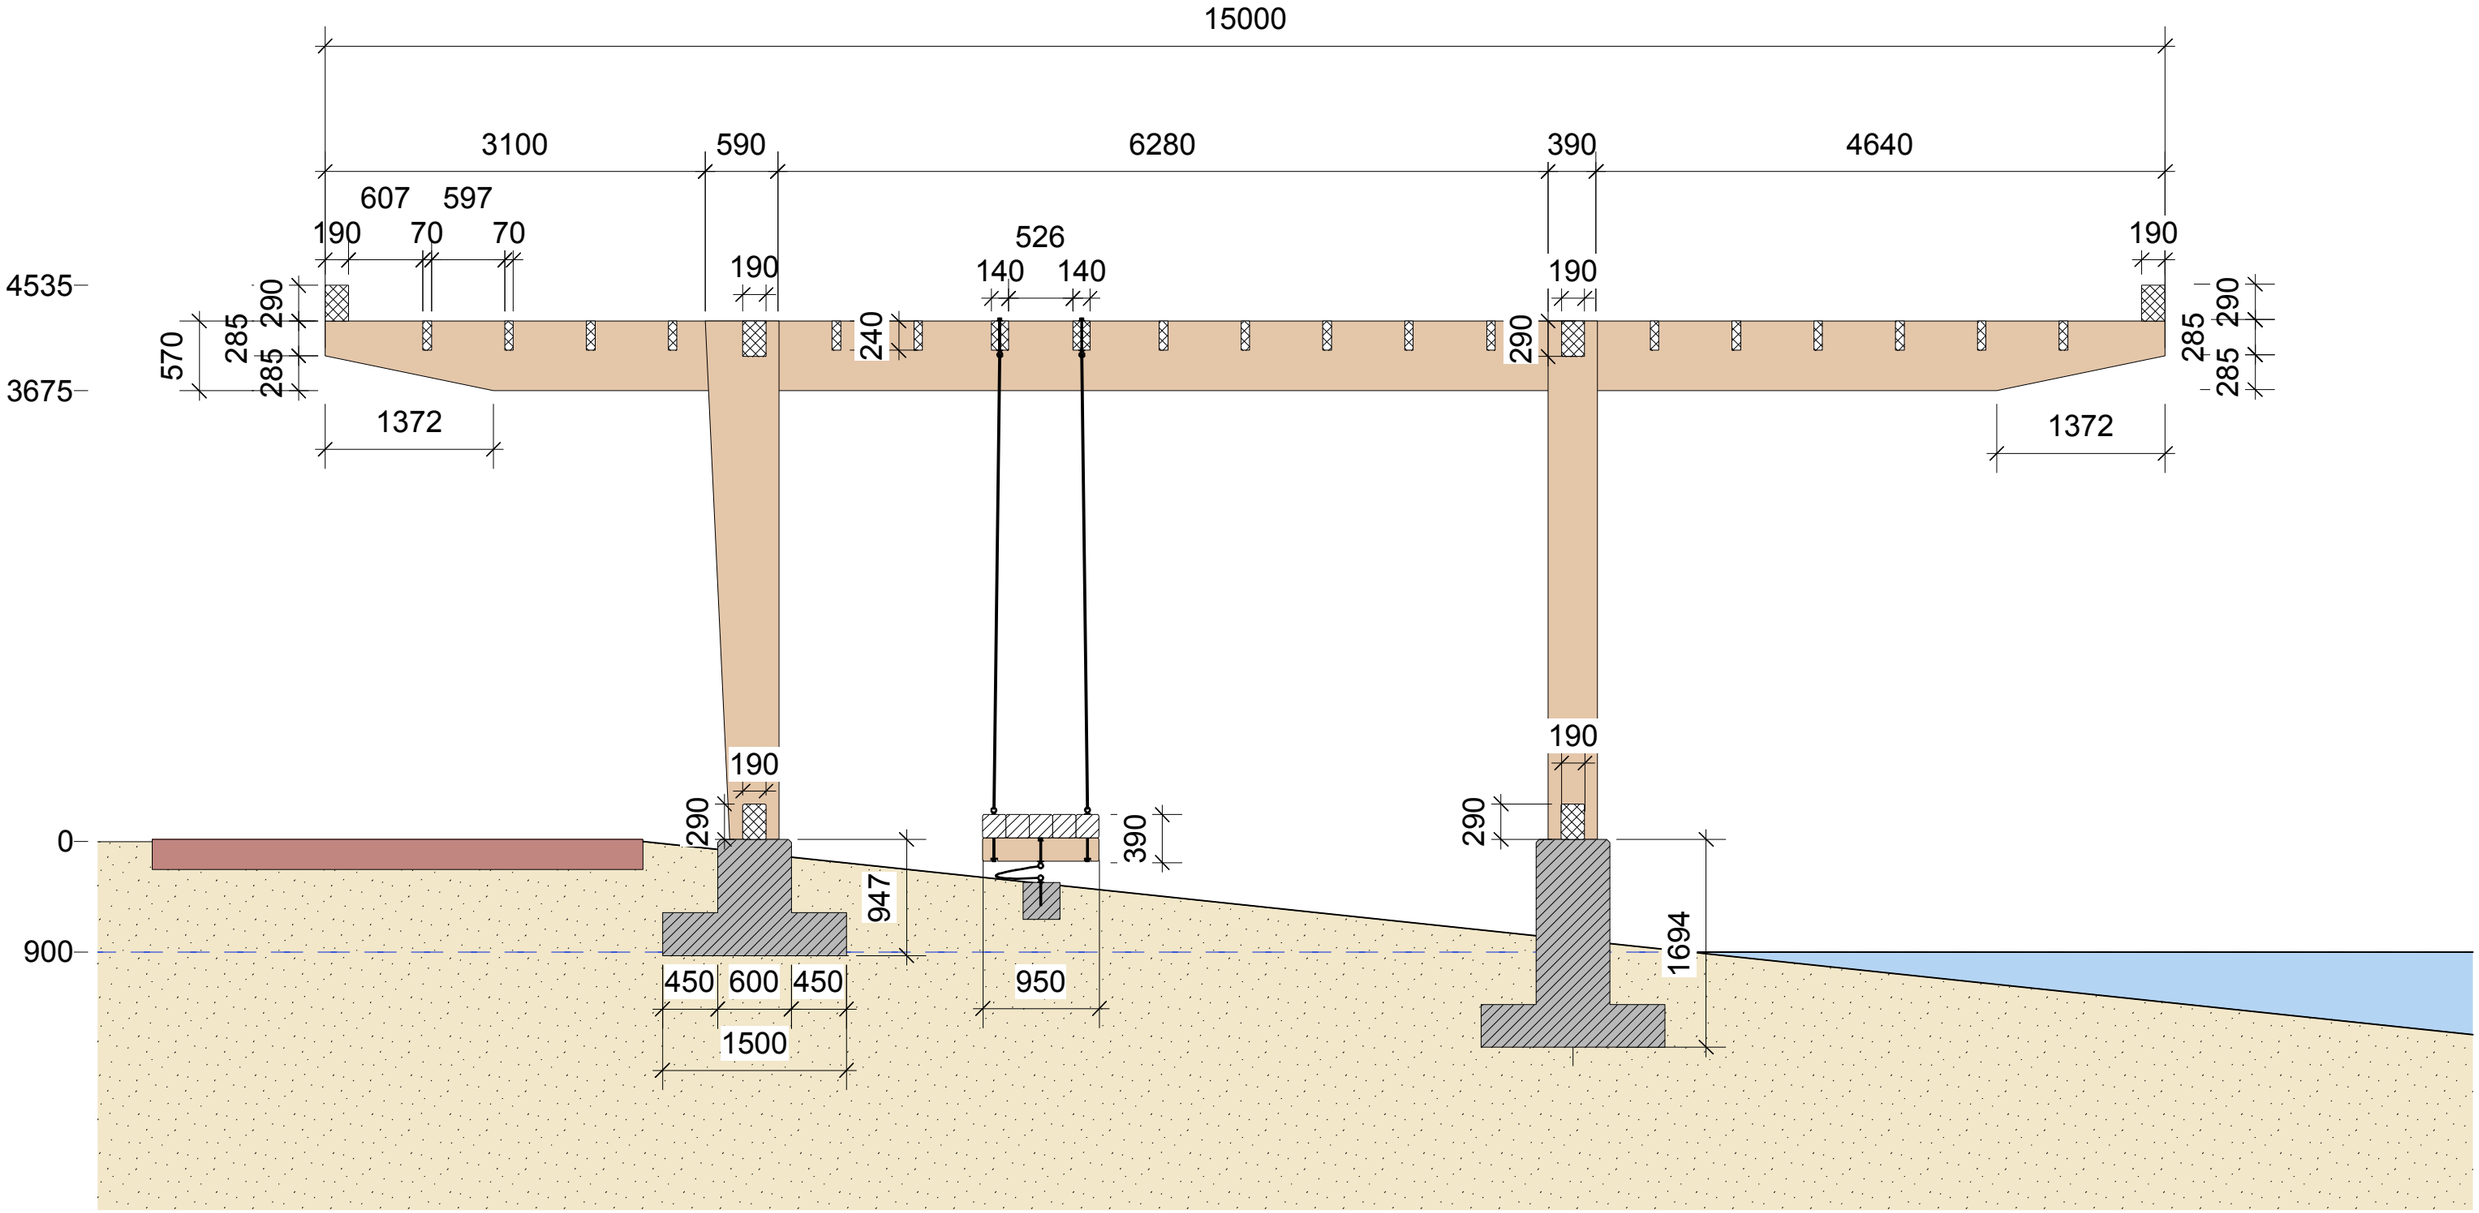


ZANDPOORT
Zijaanzicht
Azobe
Schaal 1:50
OBSERVATORIUM
Definitief ontwerp

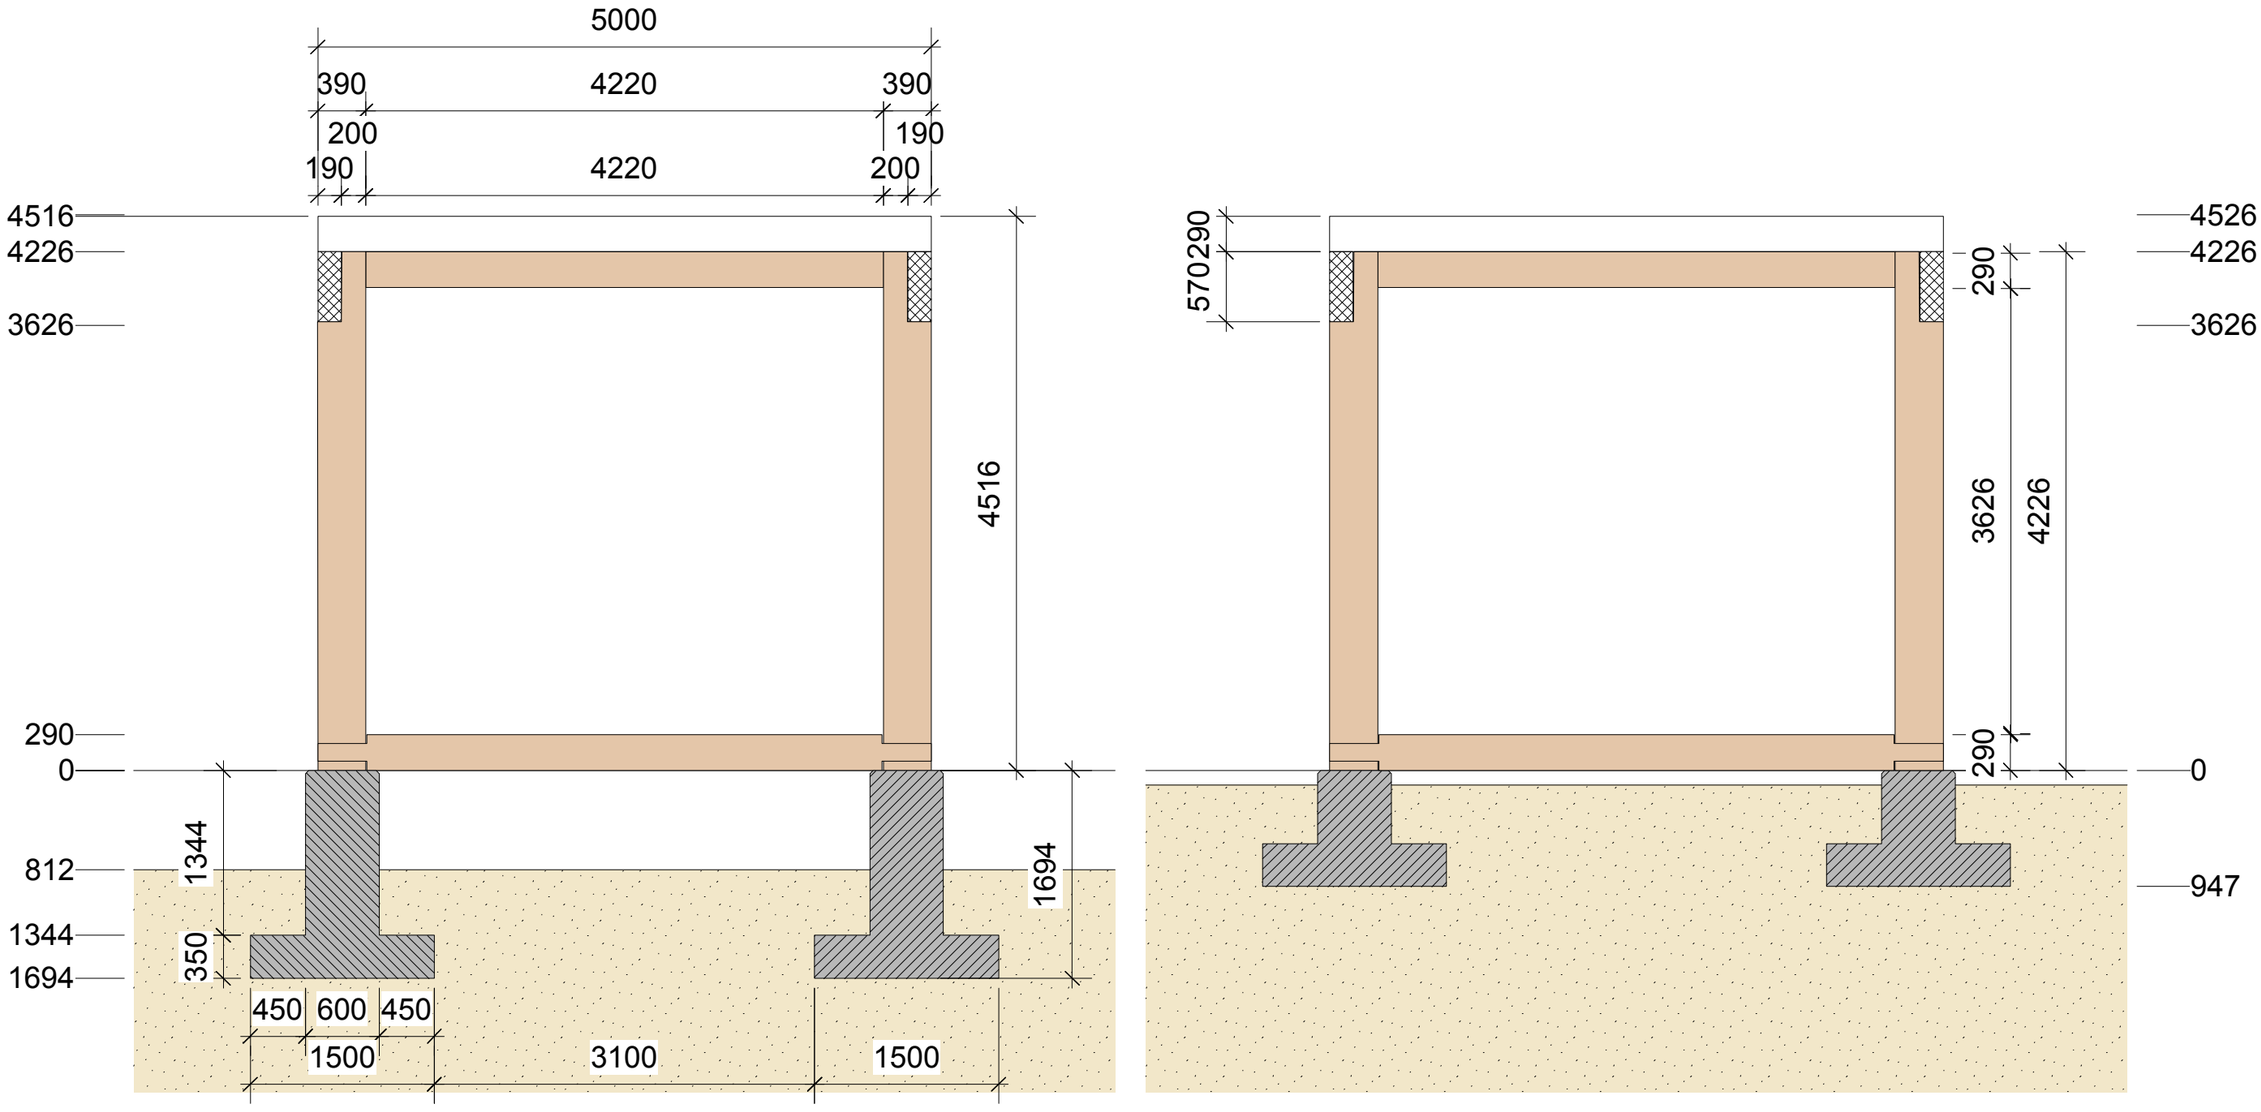

ZANDPOORT
Doorsnede
Azobe
Schaal 1:50
OBSERVATORIUM
Definitief ontwerp

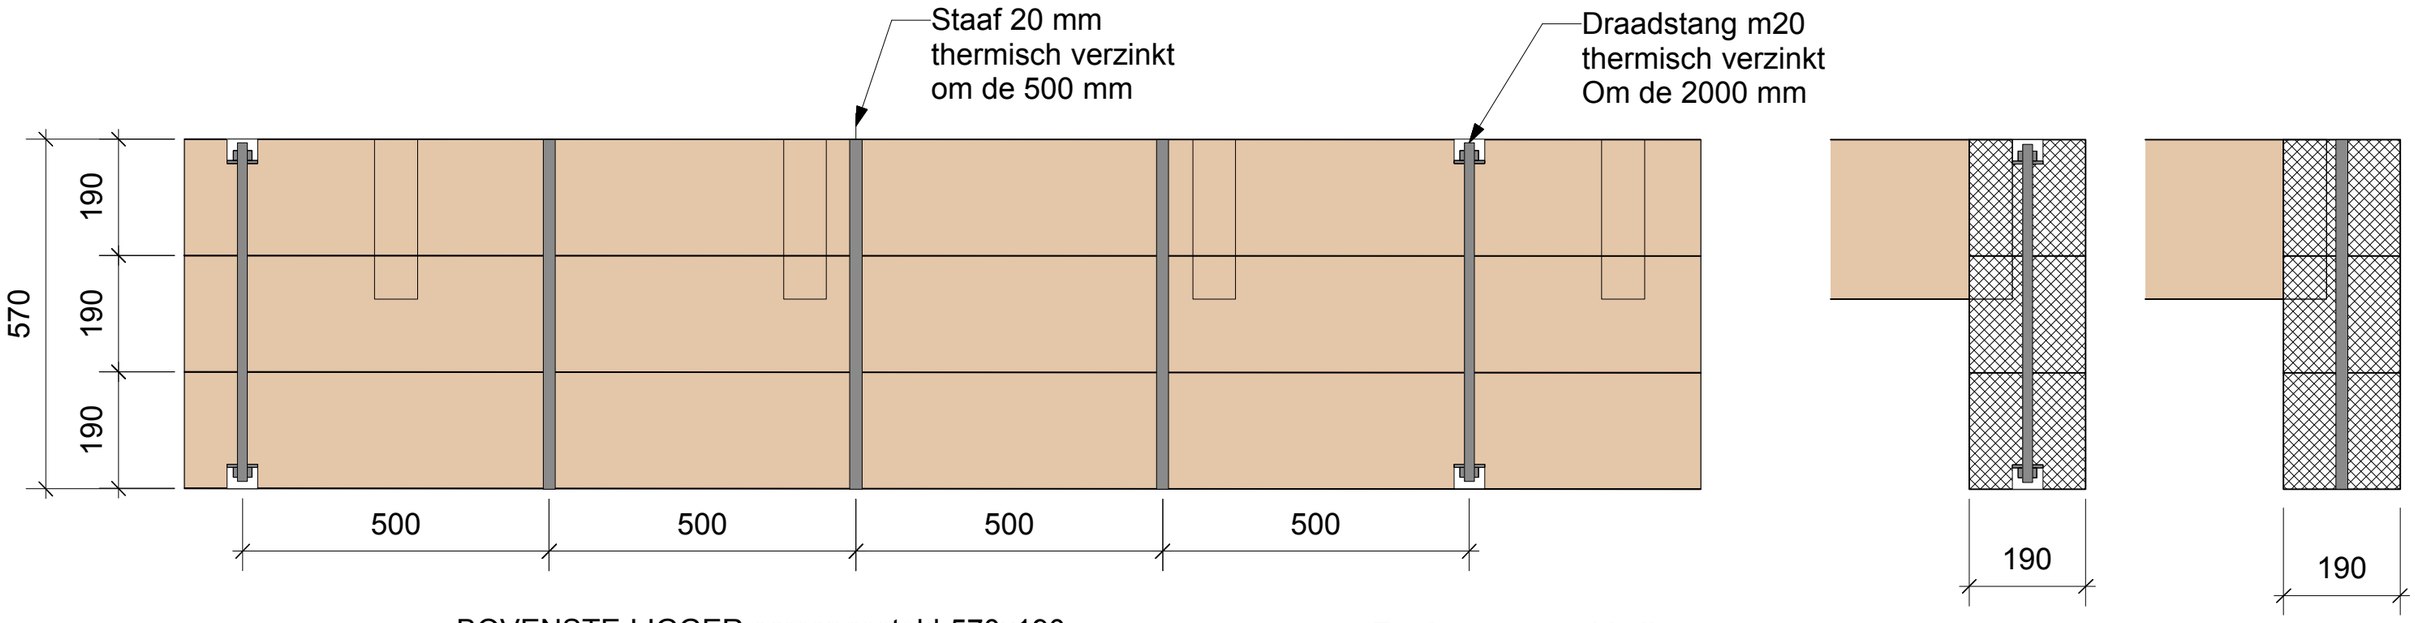



BOVENSTE LIGGER samengesteld 570x190

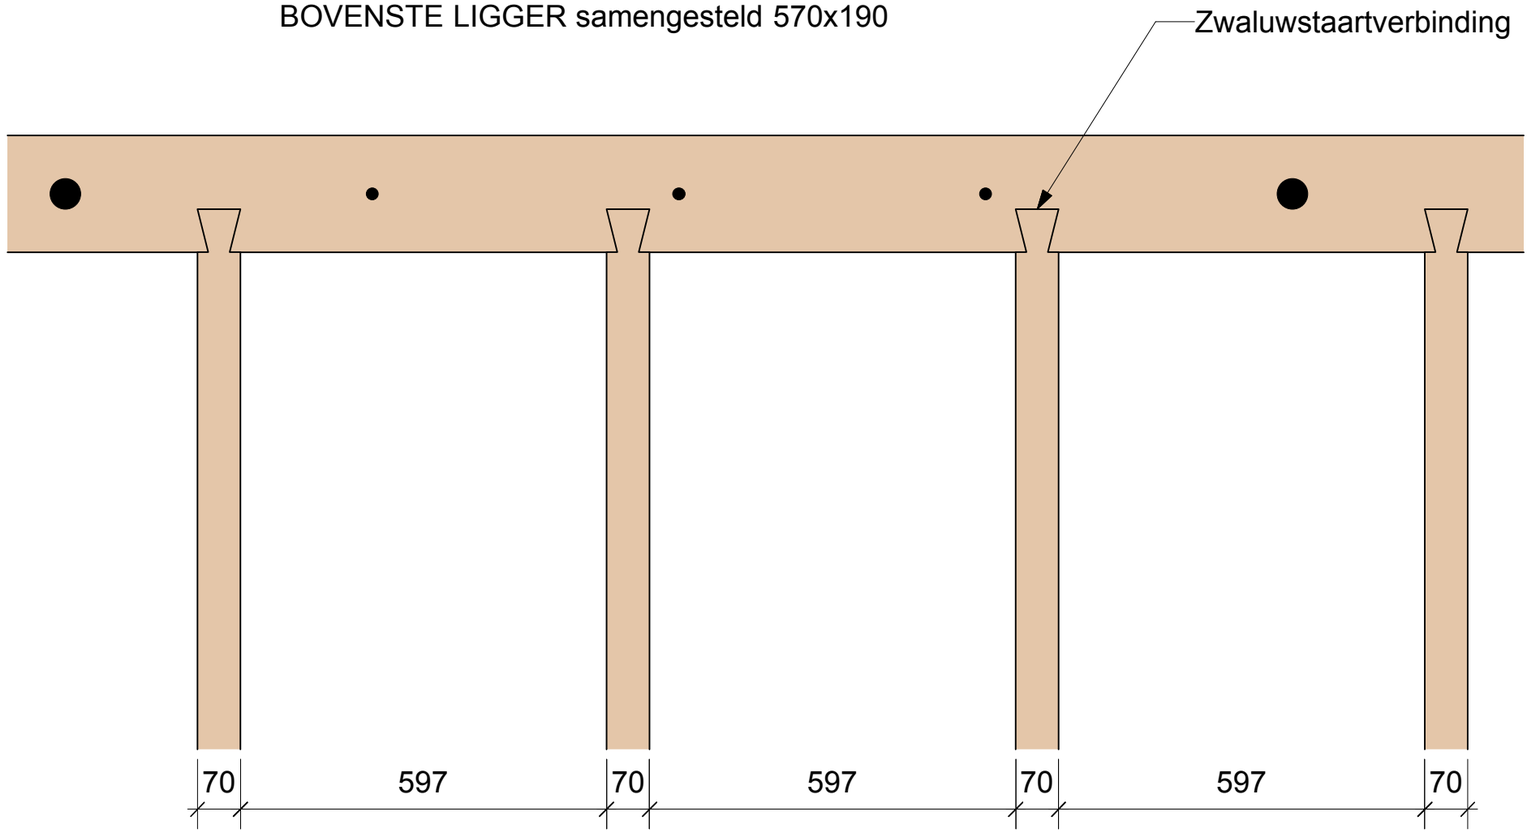



Verbinding ligger en dwarsbinten dmv zwaluwstaartverbindingen


ZANDPOORT
Detail ligger
Azobe
Schaal 1:10
OBSERVATORIUM
Definitief ontwerp

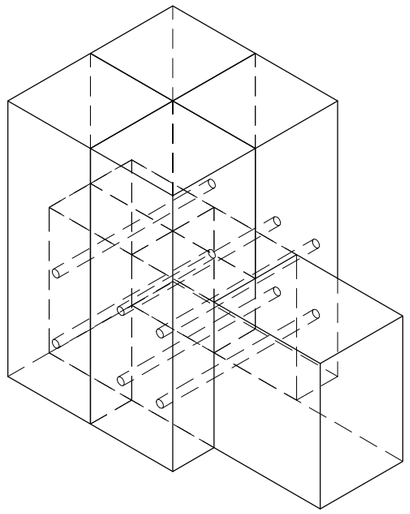


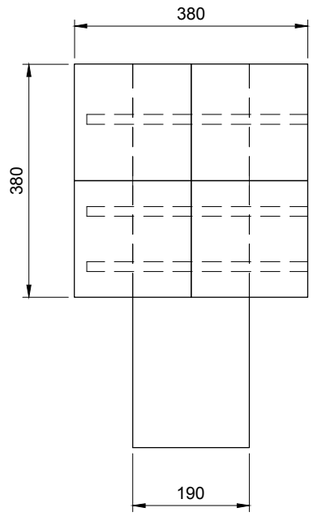

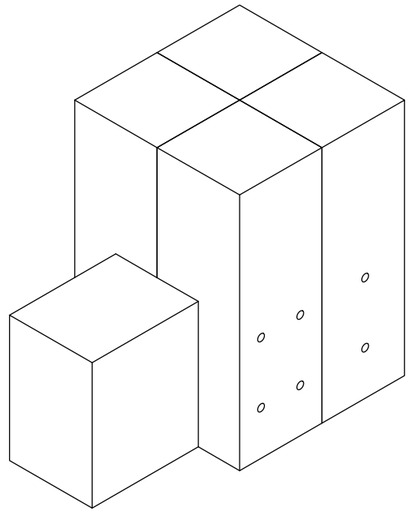

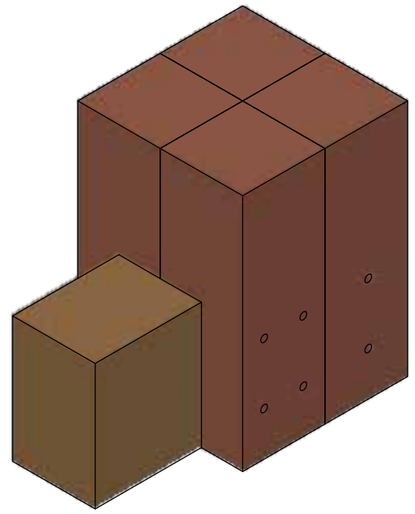

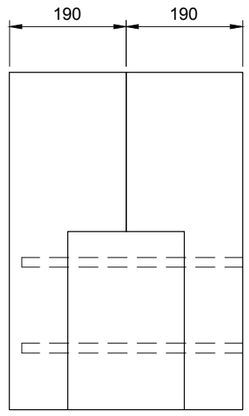

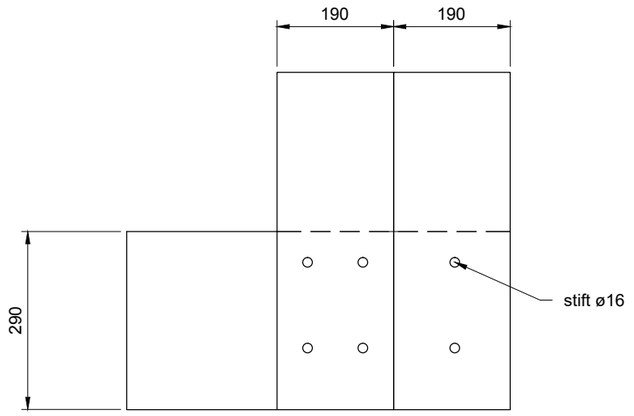

Opdrachtgever:	
Werkomschrijving:	Zandpoort
Onderdeel:	Aansluiting Kolomvoet

Wijma Kampen B.V.


Postbus 241
8260 AE Kampen (NL)


Haatlandhaven 3
8263 AS Kampen (NL)


Tel.: +31 (0)38 331 64 44
Fax: +31 (0)38 332 20 40


Internet: www.wijma.com
E-mail: wijma@wijma.com


Ordernummer: PNR00		
Tekeningnr. - Blad: M01 - D01		
Getek.:	Gecontr.:	Formaat:

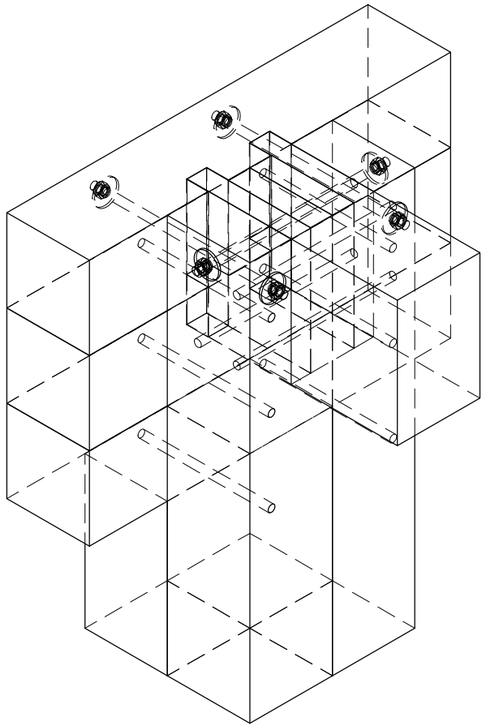


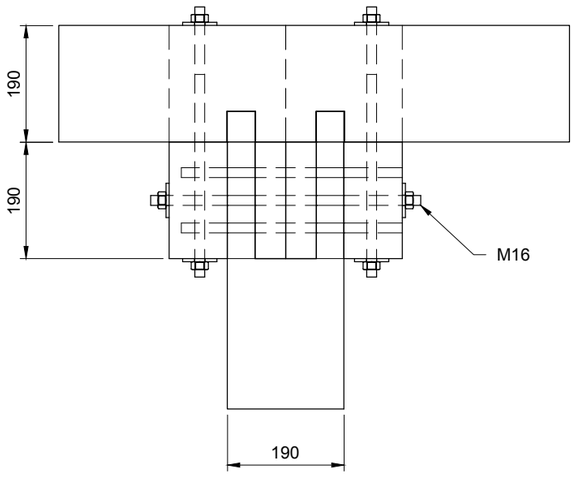

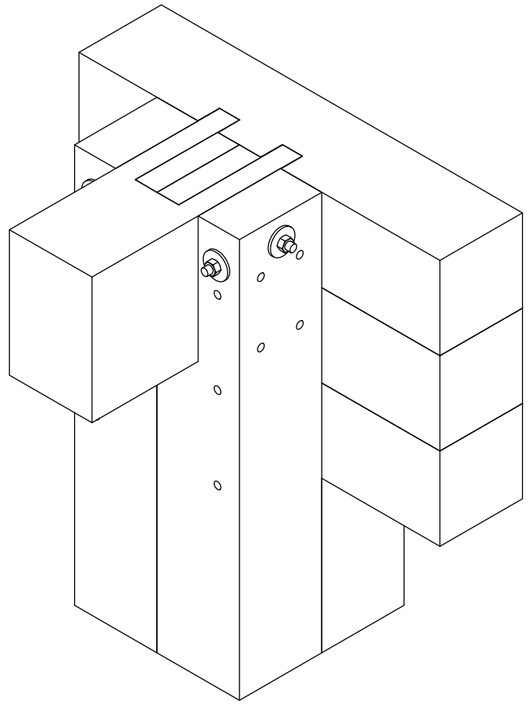

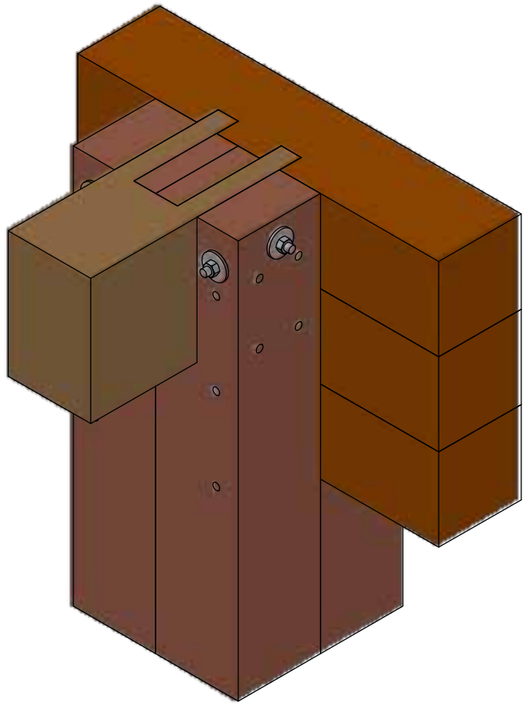

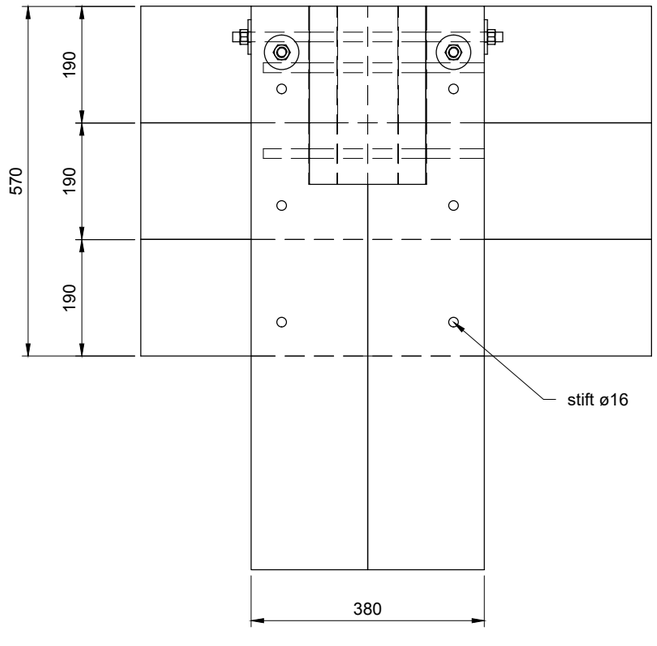

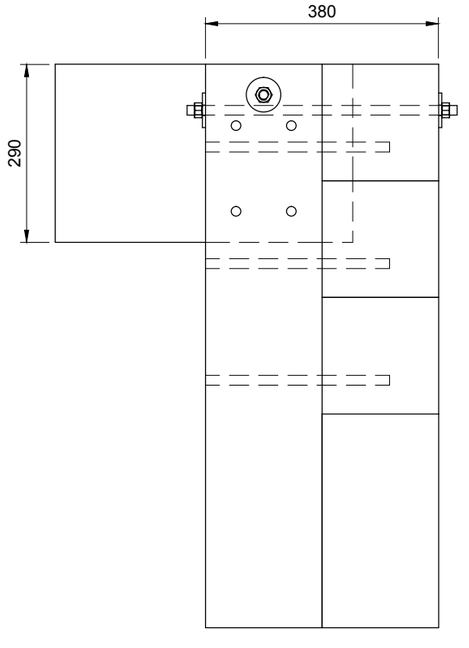

Opdrachtgever:	
Werkomschrijving:	Zandpoort
Onderdeel:	Aansluiting Kolomtop

Wijma Kampen B.V.


Postbus 241
8260 AE Kampen (NL)

Haatlandhaven 3
8263 AS Kampen (NL)

Tel.: +31 (0)38 331 64 44
Fax: +31 (0)38 332 20 40

Internet: www.wijma.com
E-mail: wijma@wijma.com

Ordernummer: PNR00		
Tekeningnr. - Blad: M01 - D02		
Getek.:	Gecontr.:	Formaat:

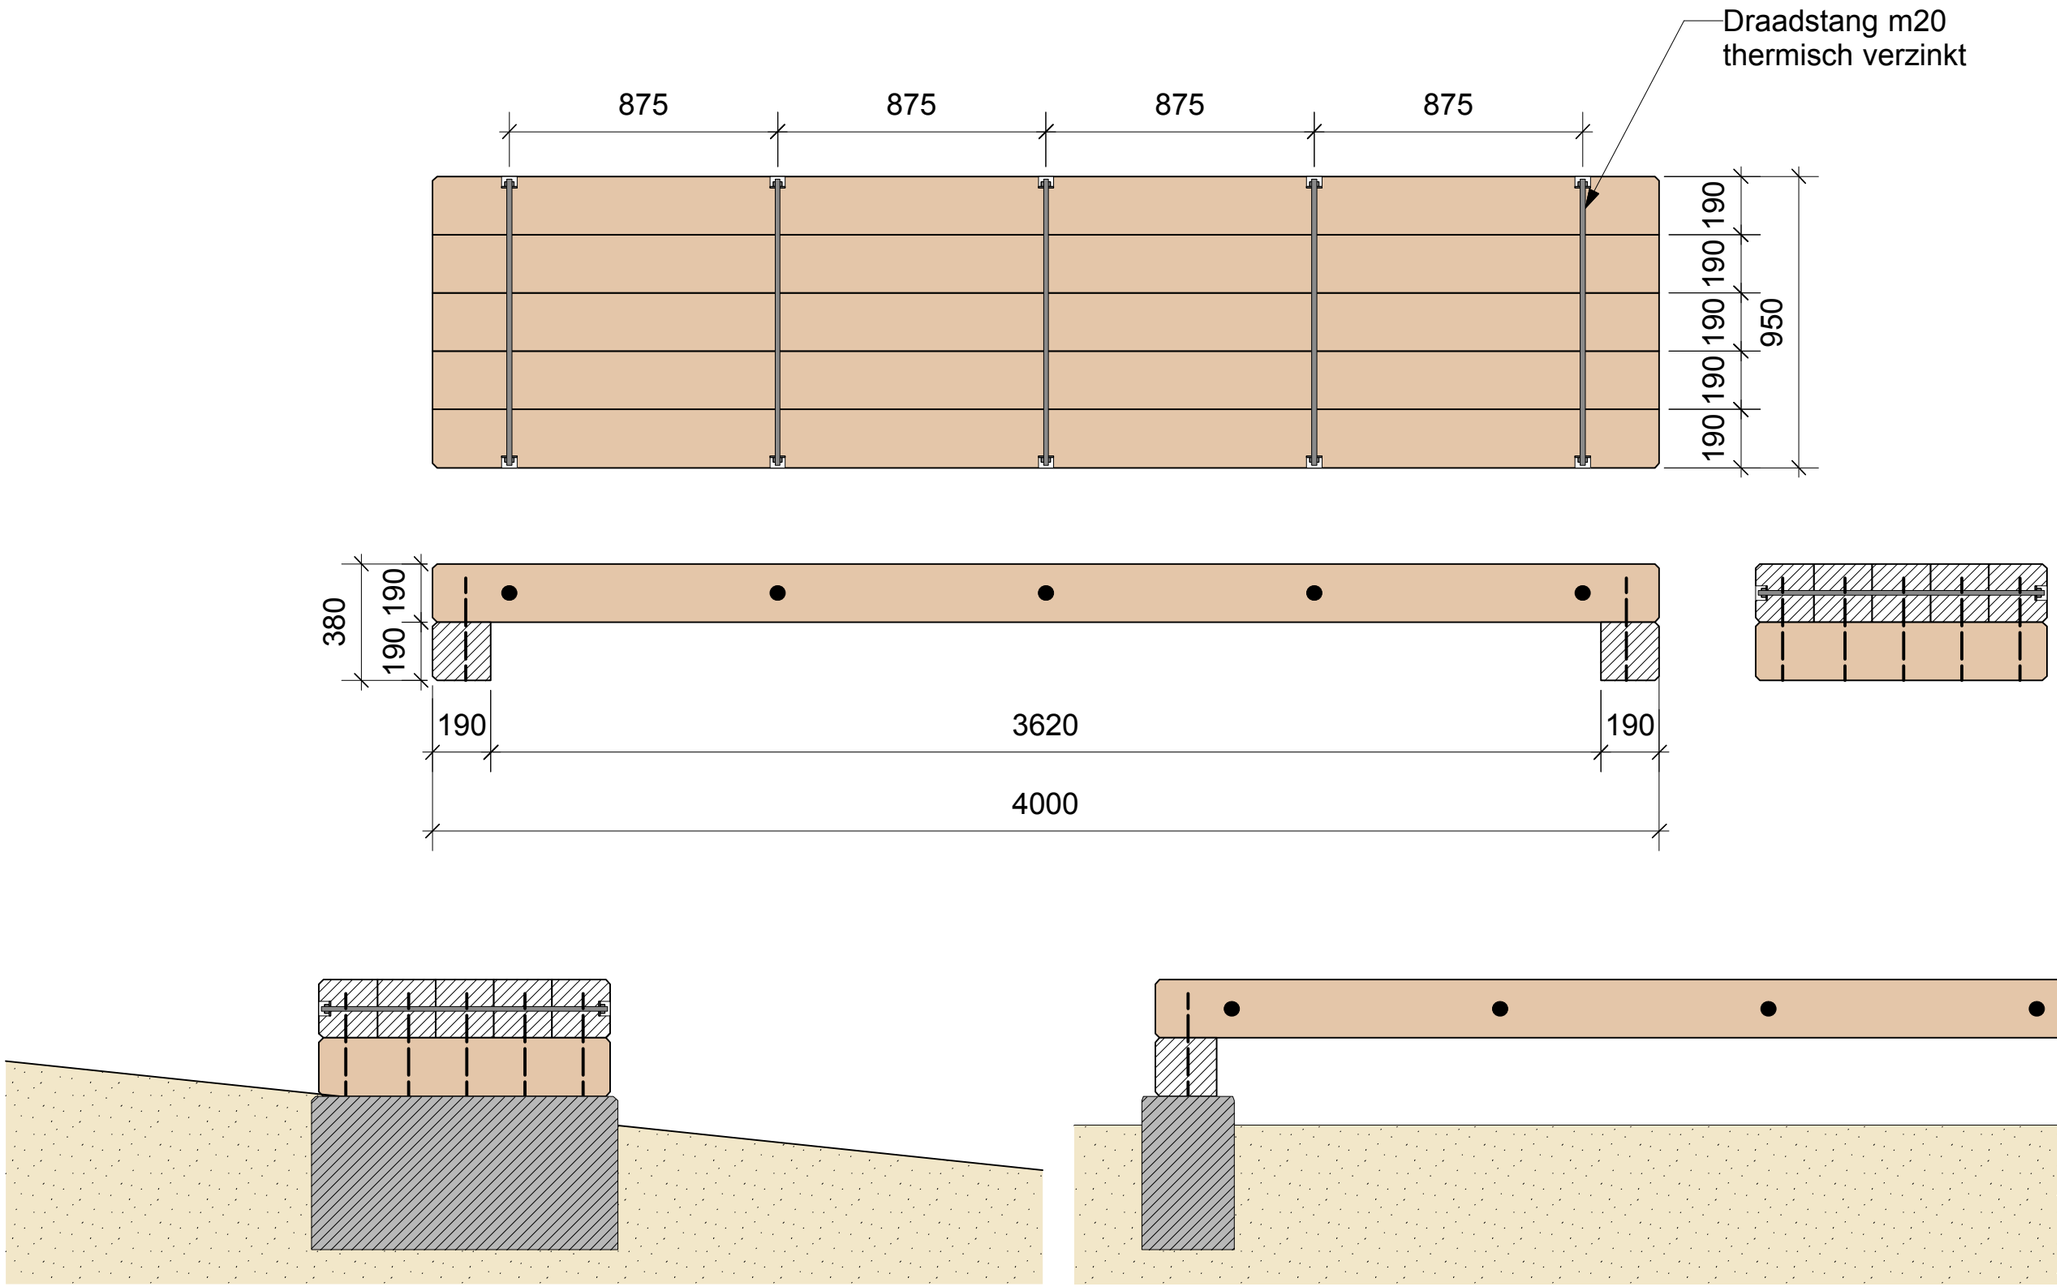

Fundering beton 1000x500x300

ZANDPOORT
Bank 4000x950x380
Douglas
Schaal 1:20
OBSERVATORIUM
Definitief ontwerp

Induline GW310 Product Informatie.

Een origineel Duits product
Remmers Induline GW 310 wordt geproduceerd in Duitsland door Remmers Gruppe GmbH en geïmporteerd door Remmers B.V. in Hoogeveen.
Het product wordt wereldwijd in miljoenen liters verkocht en toegepast op de meest uiteenlopende houtsoorten.

Het product wordt hoofdzakelijk gebruikt voor buitensituaties maar kan ook prima in binnen situaties toegepast worden.


Producteigenschappen type materiaal
Remmers Induline GW 310 is een watergedragen semifilmvormende preventieve hout beschermende impregneerlazuur voor vele houtsoorten. Beschermt het hout tegen nagenoeg alle houtaantastende organismen en weersinvloeden. Het materiaal is eenvoudig en uitstekend te verwerken en bovendien onderhouds vriendelijk


Onderhoud van met Remmers Induline GW 310
Geen enkel bouwmateriaal is onderhoudsvrij, alles staat bij buitenexpositie 24 uur per dag bloot aan allerlei invloeden. Wil men dit hout hier duurzaam, effectief en onderhoudsvriendelijk tegen beschermen, dan is Remmers Induline GW 310 hiervoor het uitgelezen product.

1. Omdat het eenvoudig is aan te brengen. 2. Onderhoudsvriendelijk is. 3. Remmers Induline GW 310 kan bogen op een jarenlange praktijkervaring.

Hierbij ons aanbevelings/onderhoudsschema voor Remmers Induline
Na ± 3 jaar het werk controleren en eventueel sterk verweerde plaatsen bijwerken. Na ± 5 jaar de reeds behandelde ondergrond met Remmers Induline GW 310 ontdoen van vuil en stof. Vervolgens 1of 2 laag/lagen Remmers Induline GW 310 opzetten en uw hout is weer beschermd voor jaren.



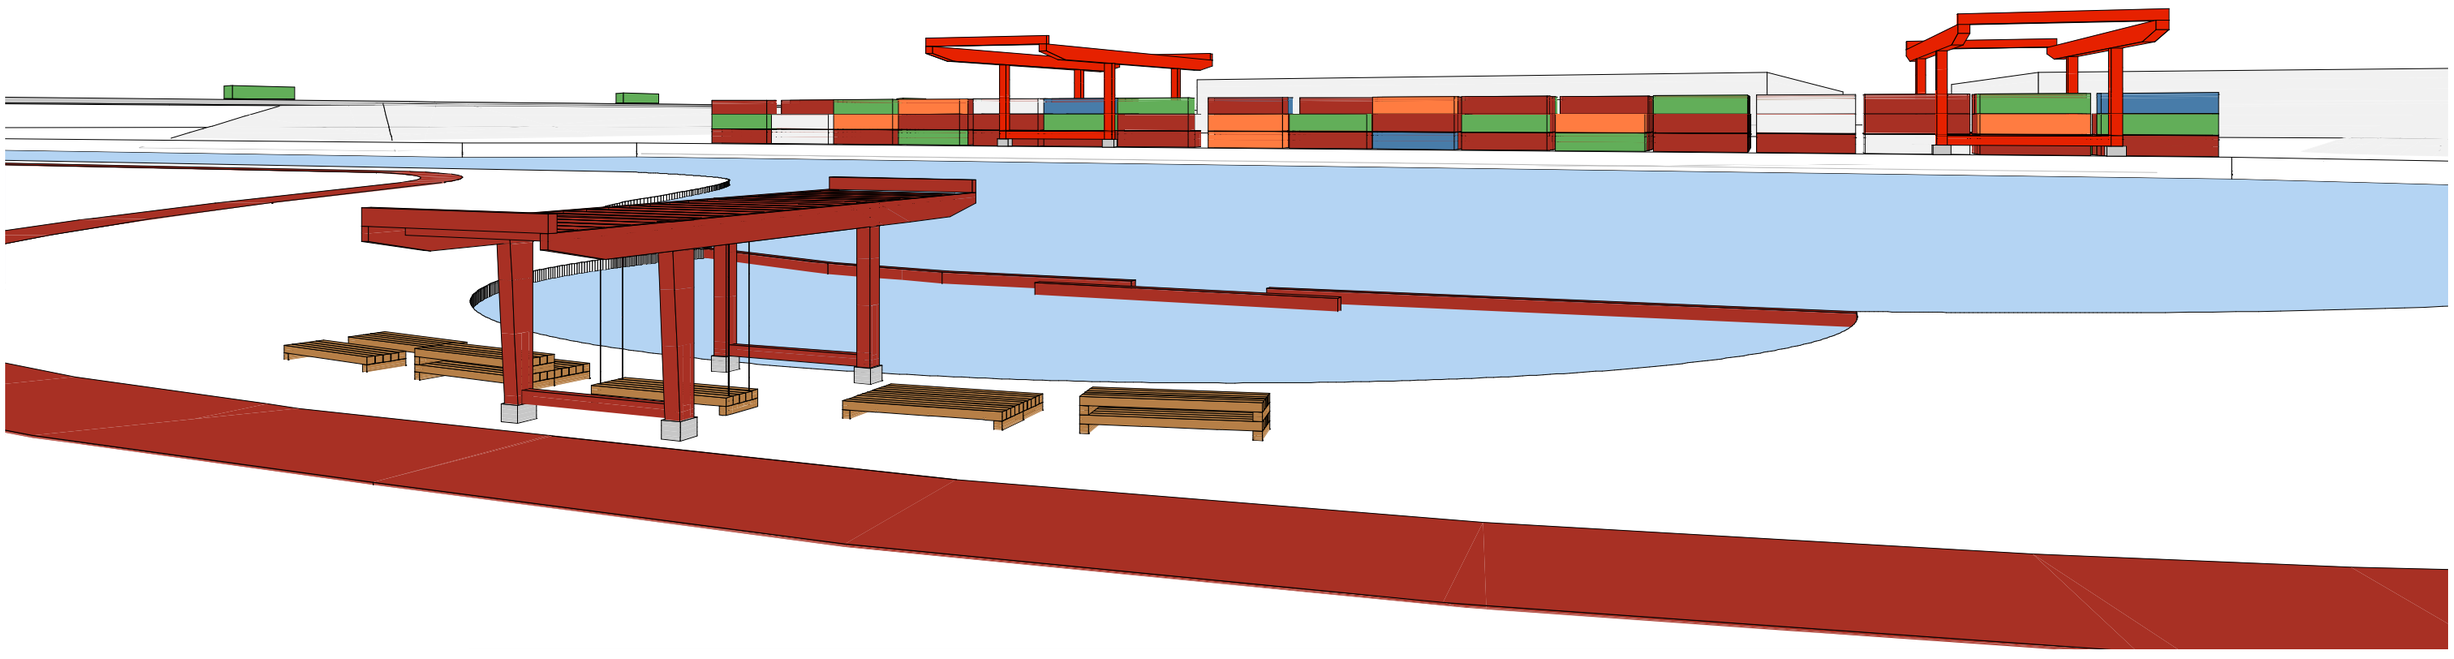

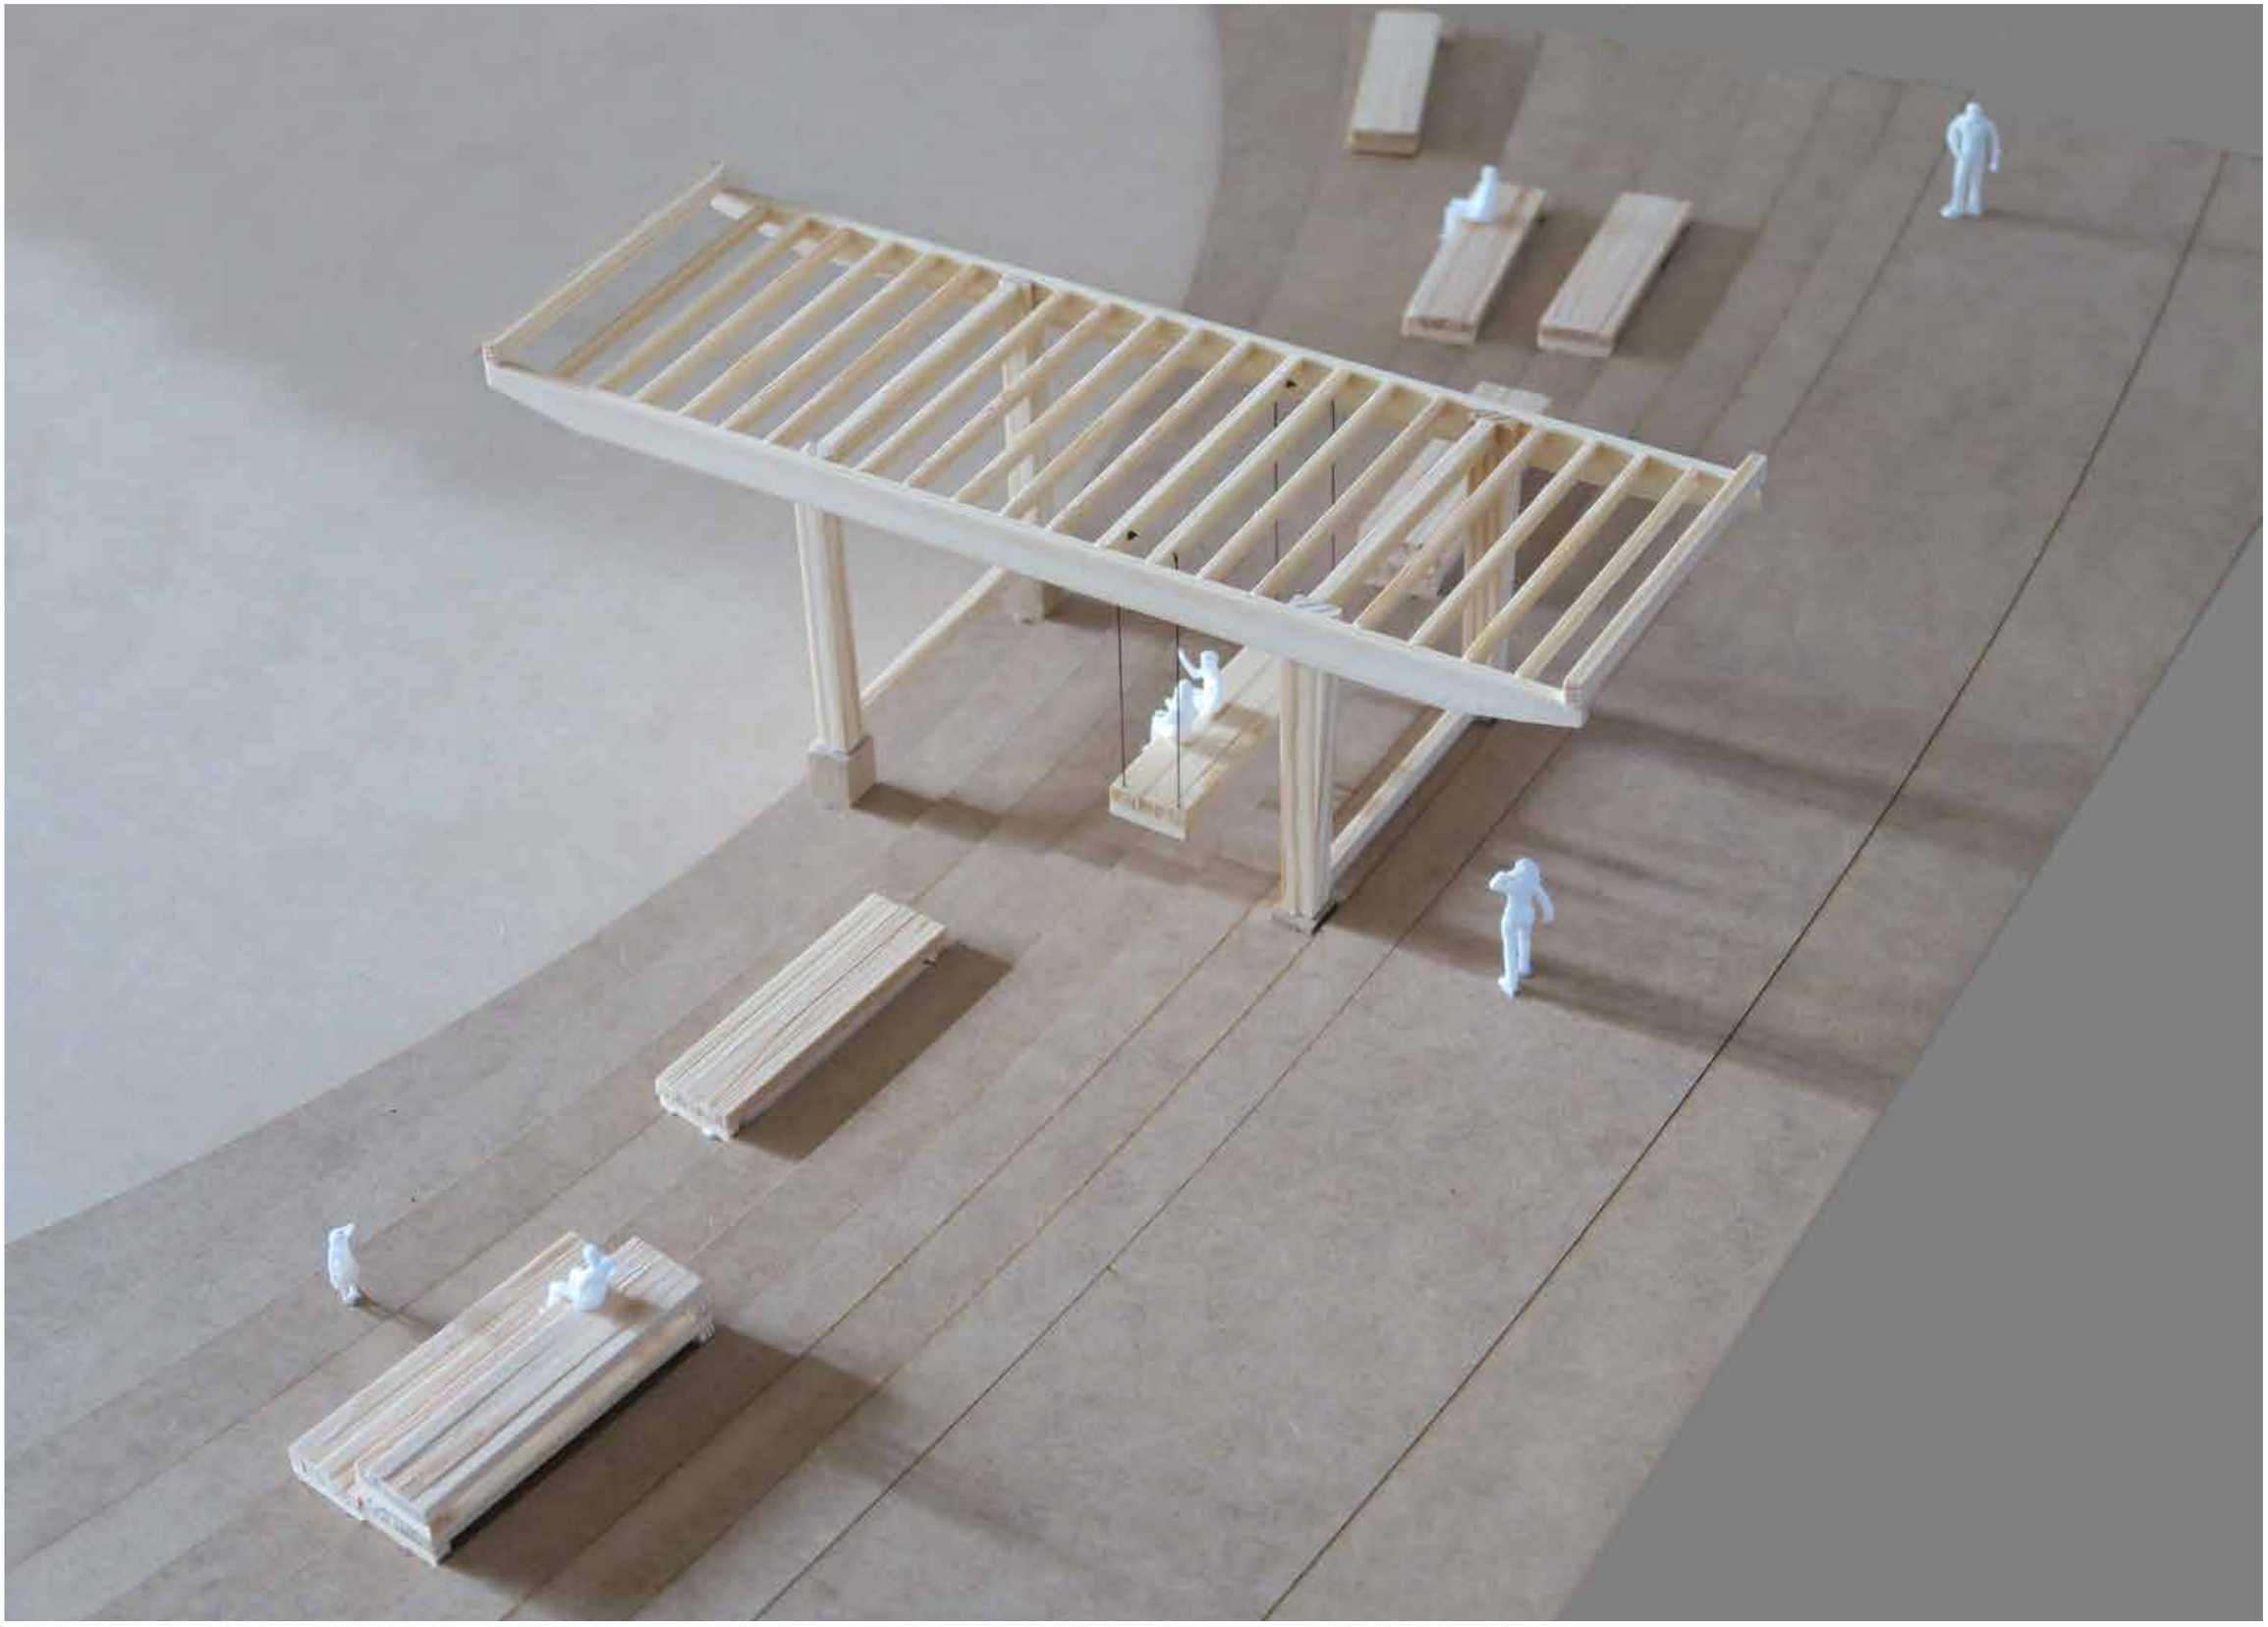

OBSERVATORIUM.ORG

Observatorium werd in 1997 in Rotterdam opgericht door kunstenaars Geert van de Camp, Andre Dekker en Ruud Reutelingsperger. Het is hun ambitie middels architecturale kunstwerken en participatieprocessen nieuwe betekenissen en passend gebruik te verlenen aan oorden in transformatie; dat kunnen pleinen,parken, industrieterreinen of stadswildernissen zijn.

Volgens Observatorium's filosofie is het publieke kunstwerk compleet als het de verbeelding stimuleert, een reflectie op de omgeving biedt en een bouwsteen voor gemeenschappelijkheid is. De iconische en symbolische werking gaat hand in hand met een vanzelfsprekend onvoorgeschreven gebruik van het beeld en bieden veelal gelegenheid afzondering en reflectie. Het oeuvre van kunst in de openbare ruimte varieert van grootschalig en permanent tot klein en tijdelijk; het maakt vrijwel altijd deel uit van stedelijke of landschappelijke gebiedsontwikkeling. In het ene geval loopt het kunstwerk vooruit op de transformatie, in het andere zet het de kroon op het werk; maar het is altijd een gastvrij oord, dat de blik op de omgeving scherpt.

Kunst Sinds 2009 is de deelname aan grootschalige beeldenroutes wezenlijk bestanddeel van het portfolio. Voor de triënnale Emscherkunst in het Ruhrgebied is de mobiele, levende brug Warten auf den Fluss gemaakt; en voor het kunstparcours Estuaire van Nantes naar Saint Nazaire het grote kunstwerk Péage Sauvage op de grens van stadswildernis en stadsuitbreiding. Parken In het Ruhrgebied heeft Observatorium in samenwerking met landschapsarchitecten twee parken ontworpen en daarvoor kunstwerken gemaakt: Halde Norddeutschland bij Neukirchen-Vluyn en het UNESCOwerelderfgoed Zollverein in Essen.

Boeken In 2010 is het boek Big Pieces of Time verschenen, dat aan de hand van twaalf projecten twaalf stellingen voor kunst in de openbare ruimte poneert. In 2011 verscheen het boek Warten auf den Fluss, over het gelijknamige paviljoen,waarin dromen en toekomstperspectieven voor een postindustriële woestenij tot leven kwamen. In 2016 publiceerde Observatorium Der grüne Schatten, een reisgids/kunstenaarsboek en in 2017 verscheen Zollverein Park – Staub, Stille Spektakel, een parkgids annex proeve van een eenentwintigste-eeuwse landschapsarchitectuur. In deze publicaties destilleren zij leidmotieven en theorieën uit de verslaglegging van hun ervaringen.

Lezingen Observatorium geeft regelmatig lezingen en workshops aan universiteiten en hogescholen, waarbij hun motto's voor kunst in de openbare ruimte door studenten kunst, architectuur en landschap beproefd worden.

We are always trying to evoke a contemplative moment in which the audience connects with the actual physical site and a deep sense of the condition humaine. At best, a public artwork creates a sense of place, together with a state of awe and intense attention.

Partners Maatschap Observatorium:
Geert van de Camp, Andre Dekker, Lieven Poutsma,
RuudReutelingsperger

Volmarijnstraat 114, NL-3021 XW Rotterdam
www.observatorium.org









